

26

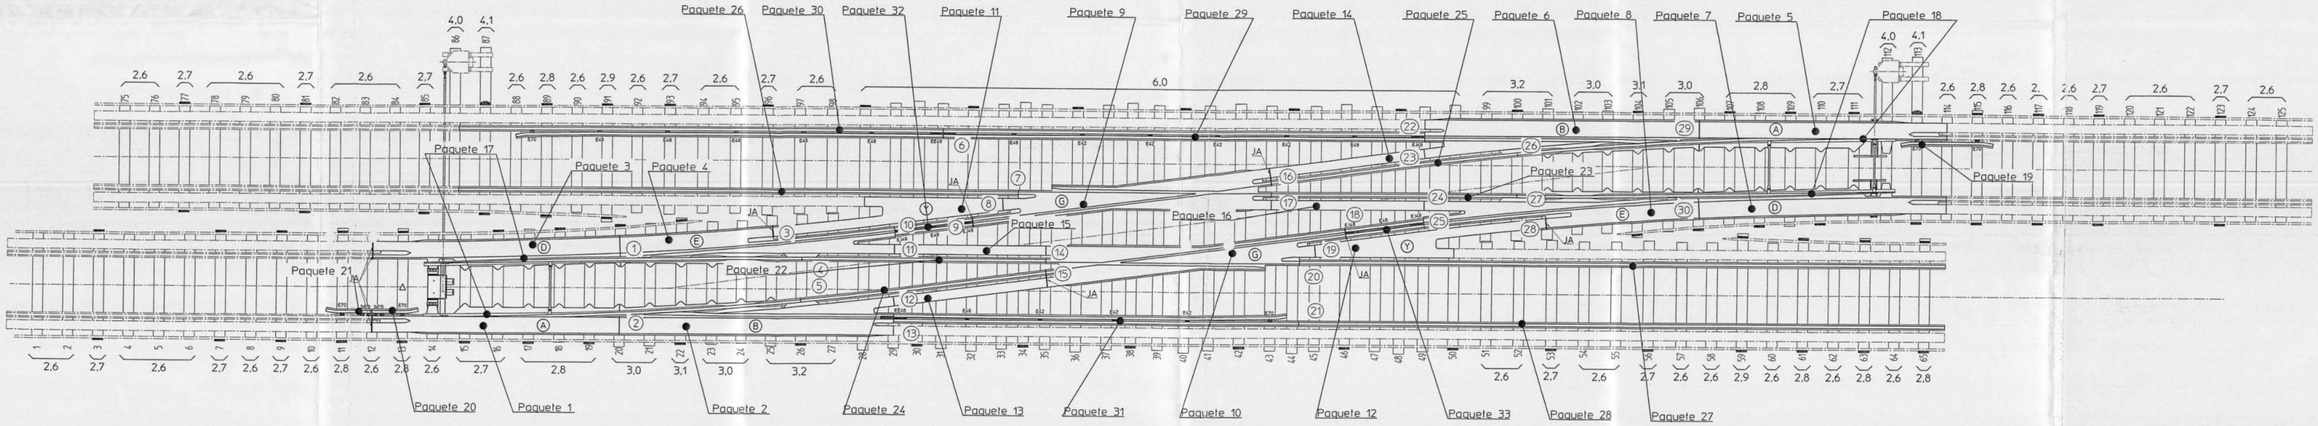

ZB1

EMPAQUE DE LOS DURMIENTES

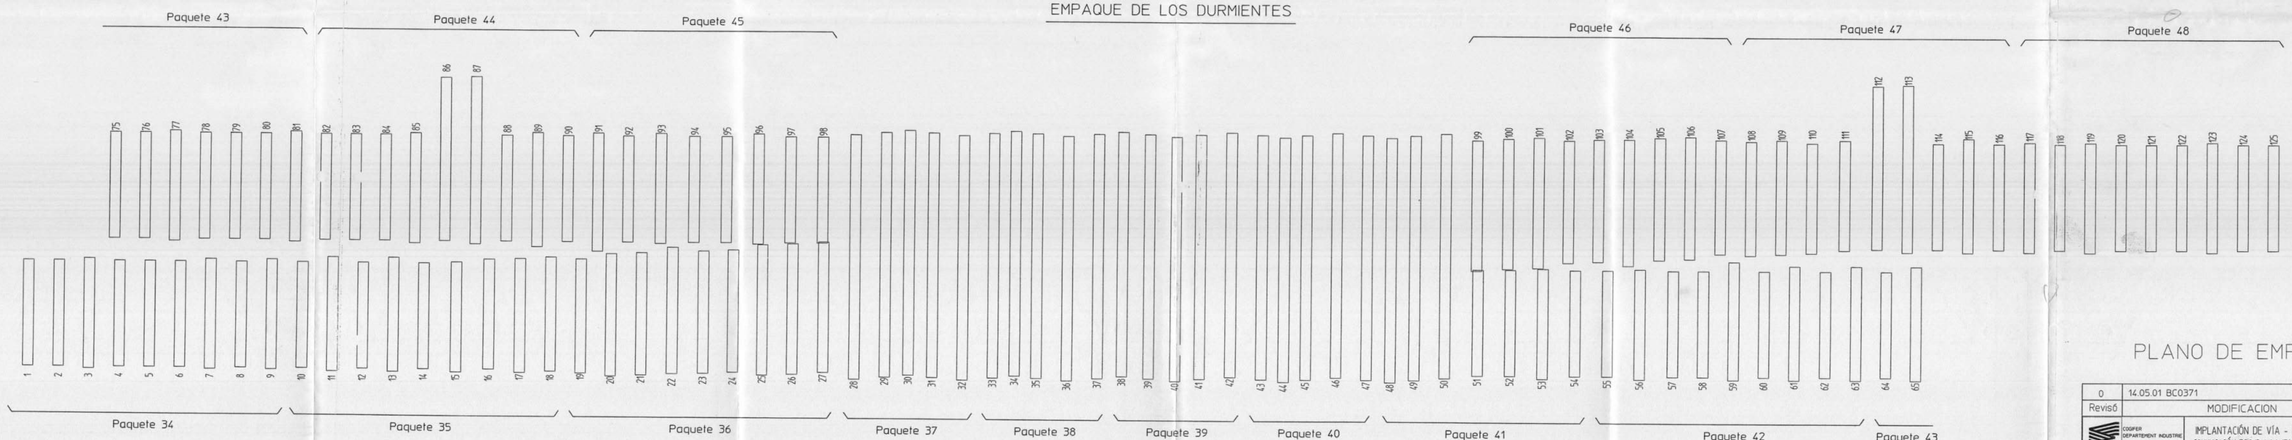

PLANO DE EMPAQUE

0	14.05.01 BC0371		Aprobó COGIFER
Revisó	MODIFICACION		
COGIFER DEPARTEMENT INDUSTRIE 45, quai de l'Ecluse 78290 Croissy-sur-Seine France	IMPLANTACIÓN DE VÍA - FIJACIÓN DE VÍA COMUNICACIÓN TG0.93 A LA I20 CON ENTREVÍA 3.15 APARATO ZB1-26 - BALDERAS - SALTO DEL AGUA		SISTEMA DE TRANSPORTE COLECTIVO Delicias No. 67 C.P. 06070 México,D.F.
Escala: 1:50	No. de Plano Cogifer: 6 117 3707 Folio 2	No. de Plano S.T.C.:	Fecha de aprobación S.T.C.
Revisó S.T.C.:		Contrato No. 001/2000	Dibujó: TRICHIES
Aprobó S.T.C.:	Vo. Bo. S.T.C.:	Autorizó S.T.C.:	Revisó: Fecha: 14-05-01