DIAGRAMA DE LAS LÍNEAS DIRECTRICES

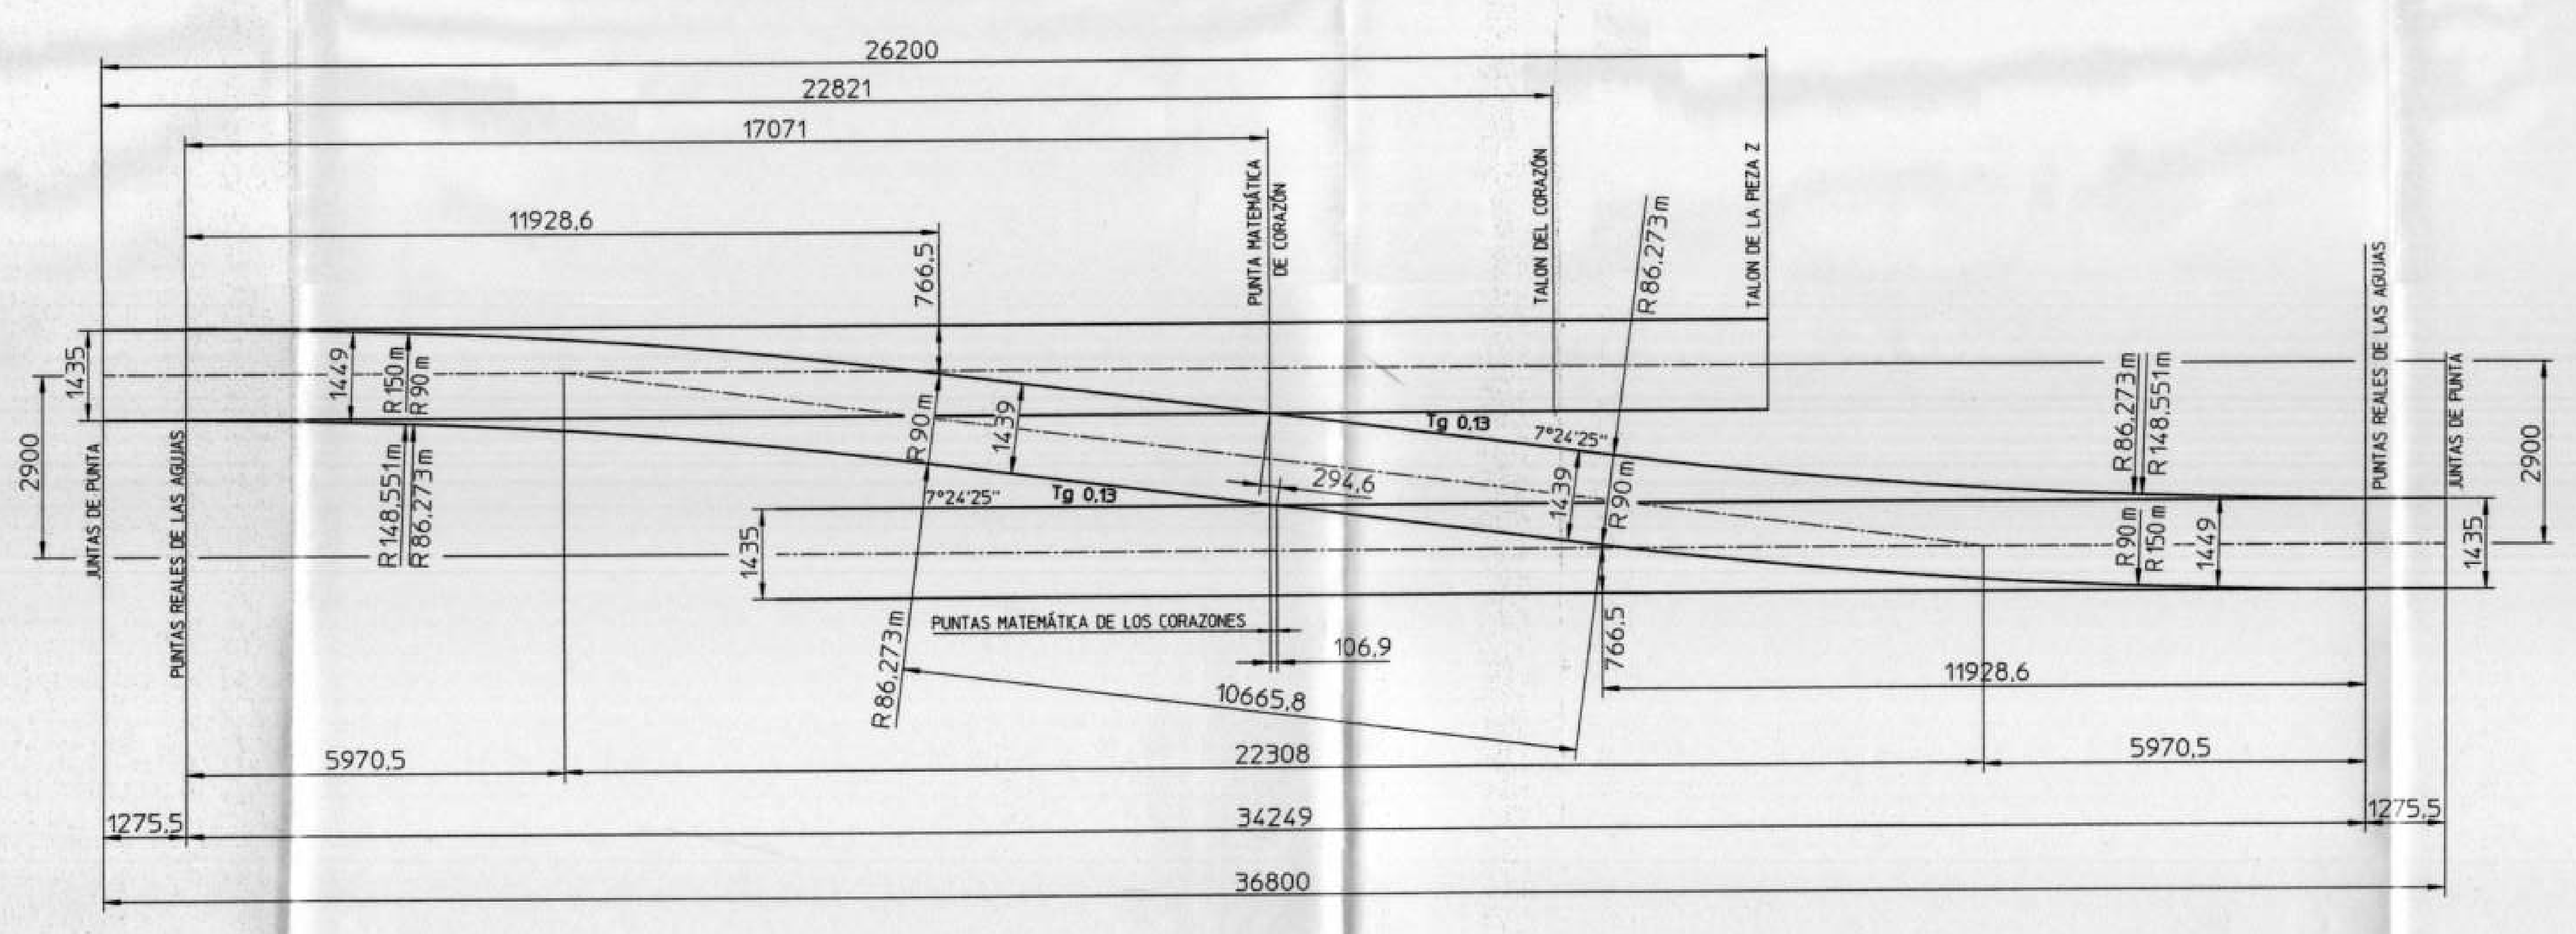

DIAGRAMA DE LAS AGUJAS

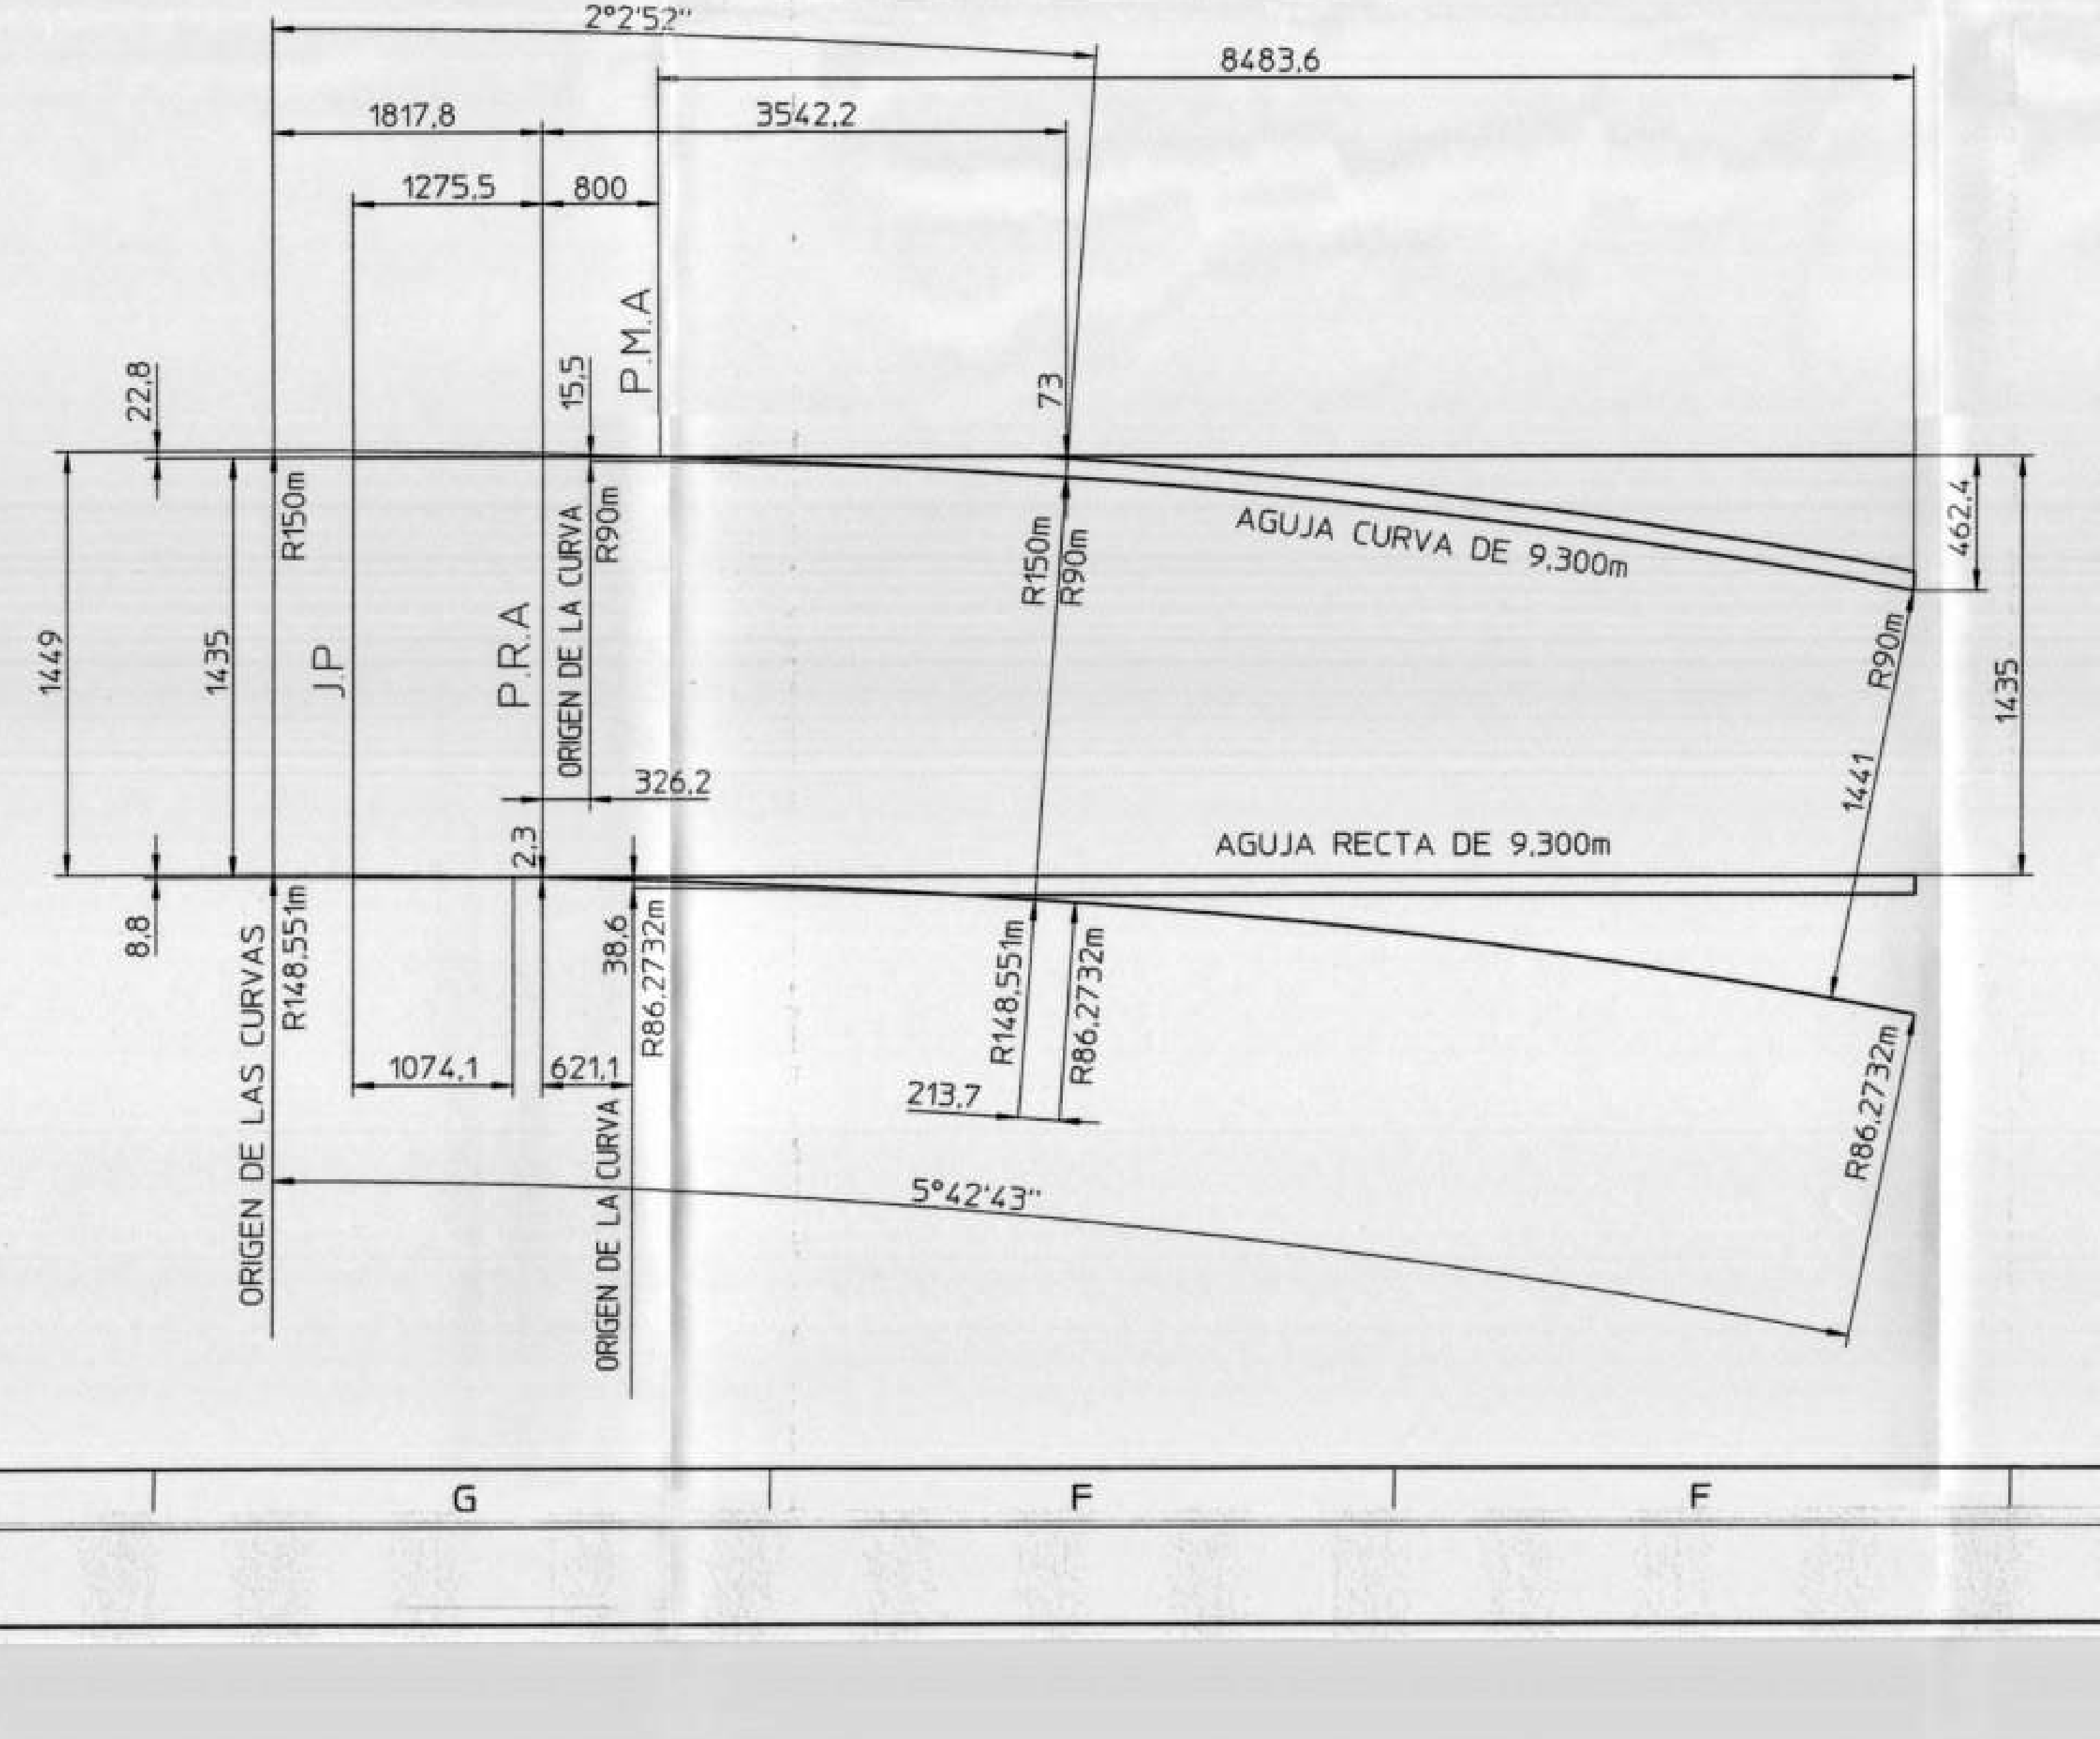

DETALLE DE LAS CABEZAS DE LOS DURMIENTES
AISLADOR SOBRE PLATILLO

Consultar plano N°6.000.0008

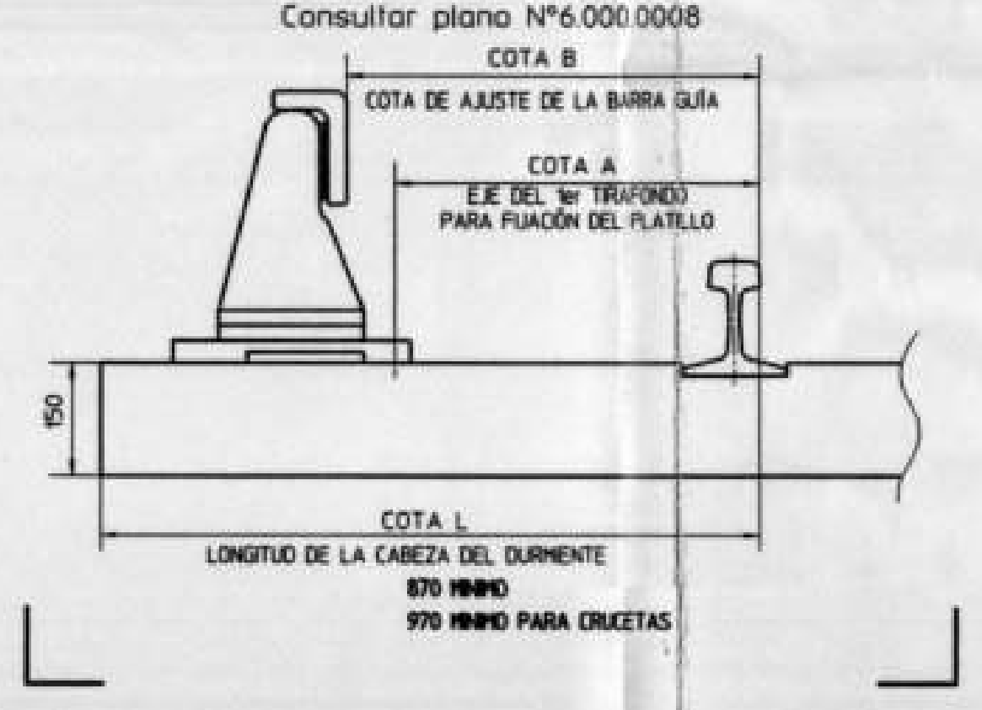
COTA B
COTA DE AJUSTE DE LA BARRA GUÍA
COTA A
EJE DEL 1er TIRAFONDO PARA FIJACIÓN DEL PLATILLO
150
COTA L
LONGITUD DE LA CABEZA DEL DURMIENTE
870 MÍNIMO
970 MÍNIMO PARA CRUCETAS

DETALLE DE LAS CABEZAS DE LOS DURMIENTES
AISLADOR SOBRE ZOCLO

Consultar plano N°6.000.0007

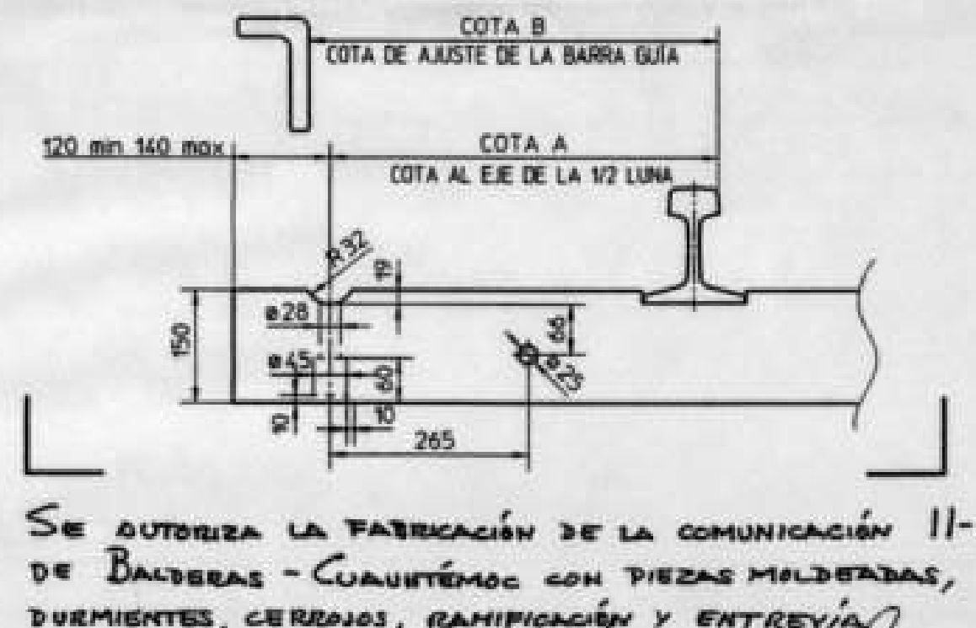

Se autoriza la fabricación de la comunicación 11-21 de Balderas - Cuauhtémoc con piezas moldeadas, durmientes, cerrojos, ramificación y entrevía indicados en este documento

Ing. A. Horacio Pereira M.
S.T.C. 19/Feb/2007

NOTA : Las piezas indicadas con líneas mixtas no forman parte del suministro.

	AUTORIZO : DGMSTC	APROBO : DGMSTC	REVISO : DGMSTC

Nbre Qty	Repère Refer.	Symbole Symbol	Désignation des pièces Item	Matière dessin ou norme Material drawing or standard	P. unit. Unit w.

Il faut pour
Requirements for

IMPLANTACIÓN DE VÍA - FIJACIÓN DE VÍA
COMUNICACIÓN TG.0,13 A LA DERECHA CON ENTREVÍA 2,9
APARATO 11-21 - BALBUENA CUAHUTEMOC - Línea 1

BALDERAS - CUAUHTÉMOC

Date	01-02-07
Dess. Drawn	KOCHER
Vérif. Checked	

Echelle Scale	Type de rail Type of rail	Poids total Total weight	Symbole Symbol
1:50	AREA 100RE PISTE 68kg		

vossloh Switch Systems

Vossloh Cogifer

N° plan Dwg N° 6 217 4343 0

Modifications: 0 01.02.07 BC0580

CE PLAN EST NOTRE PROPRIETE EXCLUSIVE
Il ne peut être reproduit ni communiqué à des tiers sans notre autorisation écrite (Loi du 11 mars 1957)
THIS DRAWING IS CONFIDENTIAL AND THE COPYRIGHT OF Vossloh Cogifer
And may not be reproduced in any form whatsoever without our written authority (Loi du 11 march 1957)