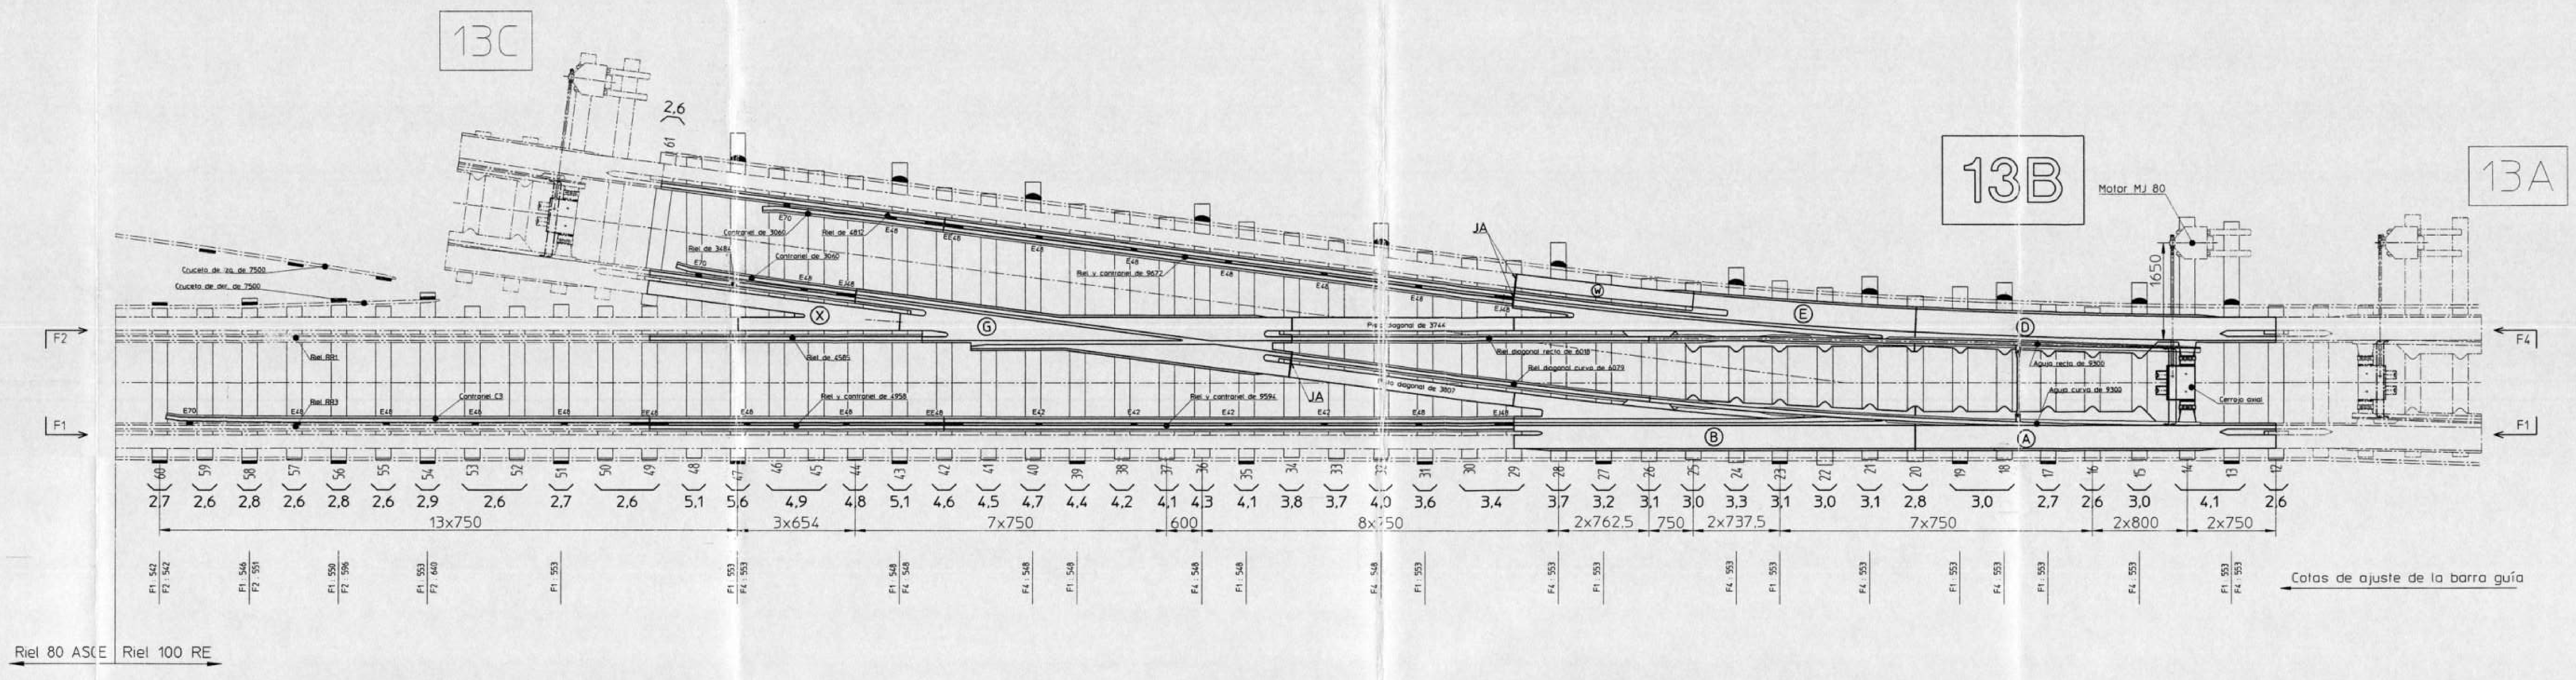

MATERIAL AGREGADO	
Durmiente de 2,60 sin entallado	1,2,4,5,6,8,10,63,65,68,70 y 72
Durmiente de 2,70 sin entallado	3,7,9,62 y 64
Durmiente de 2,80 sin entallado	11,69 y 71
Durmiente de 2,90 sin entallado	67

DIAGRAMA DE LAS LÍNEAS DIRECTRICES

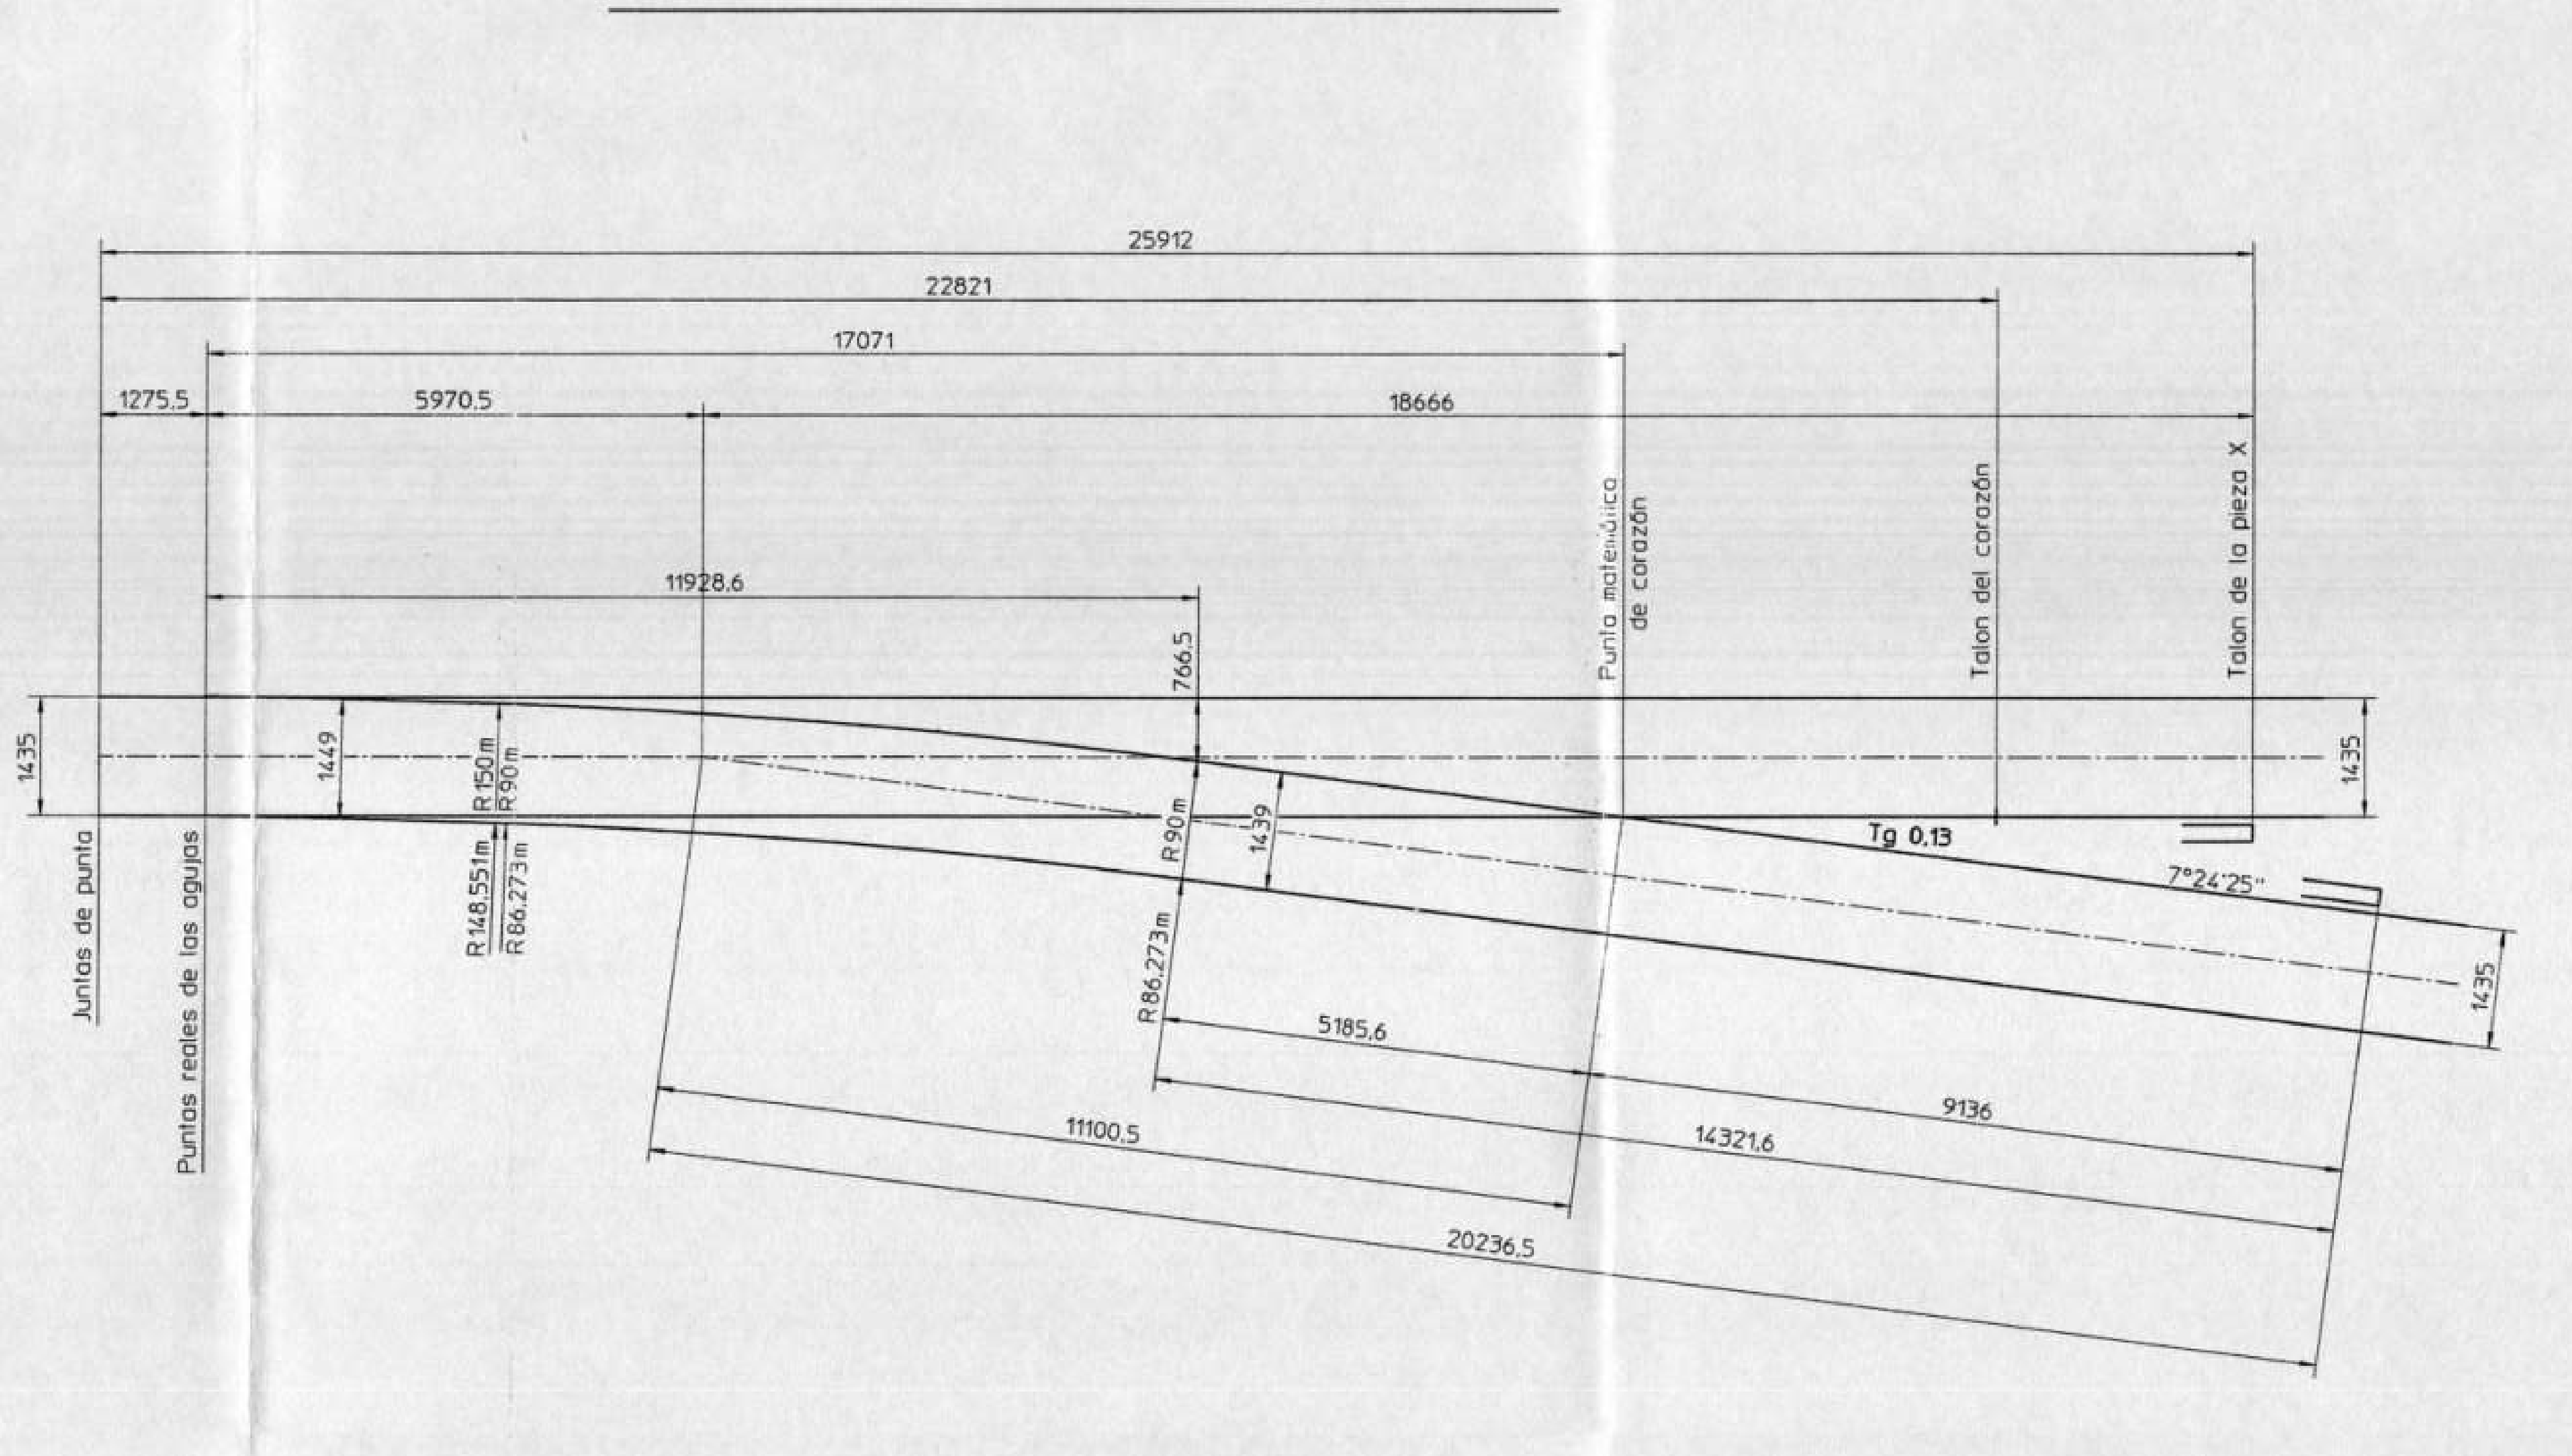

DIAGRAMA DE LAS AGUJAS

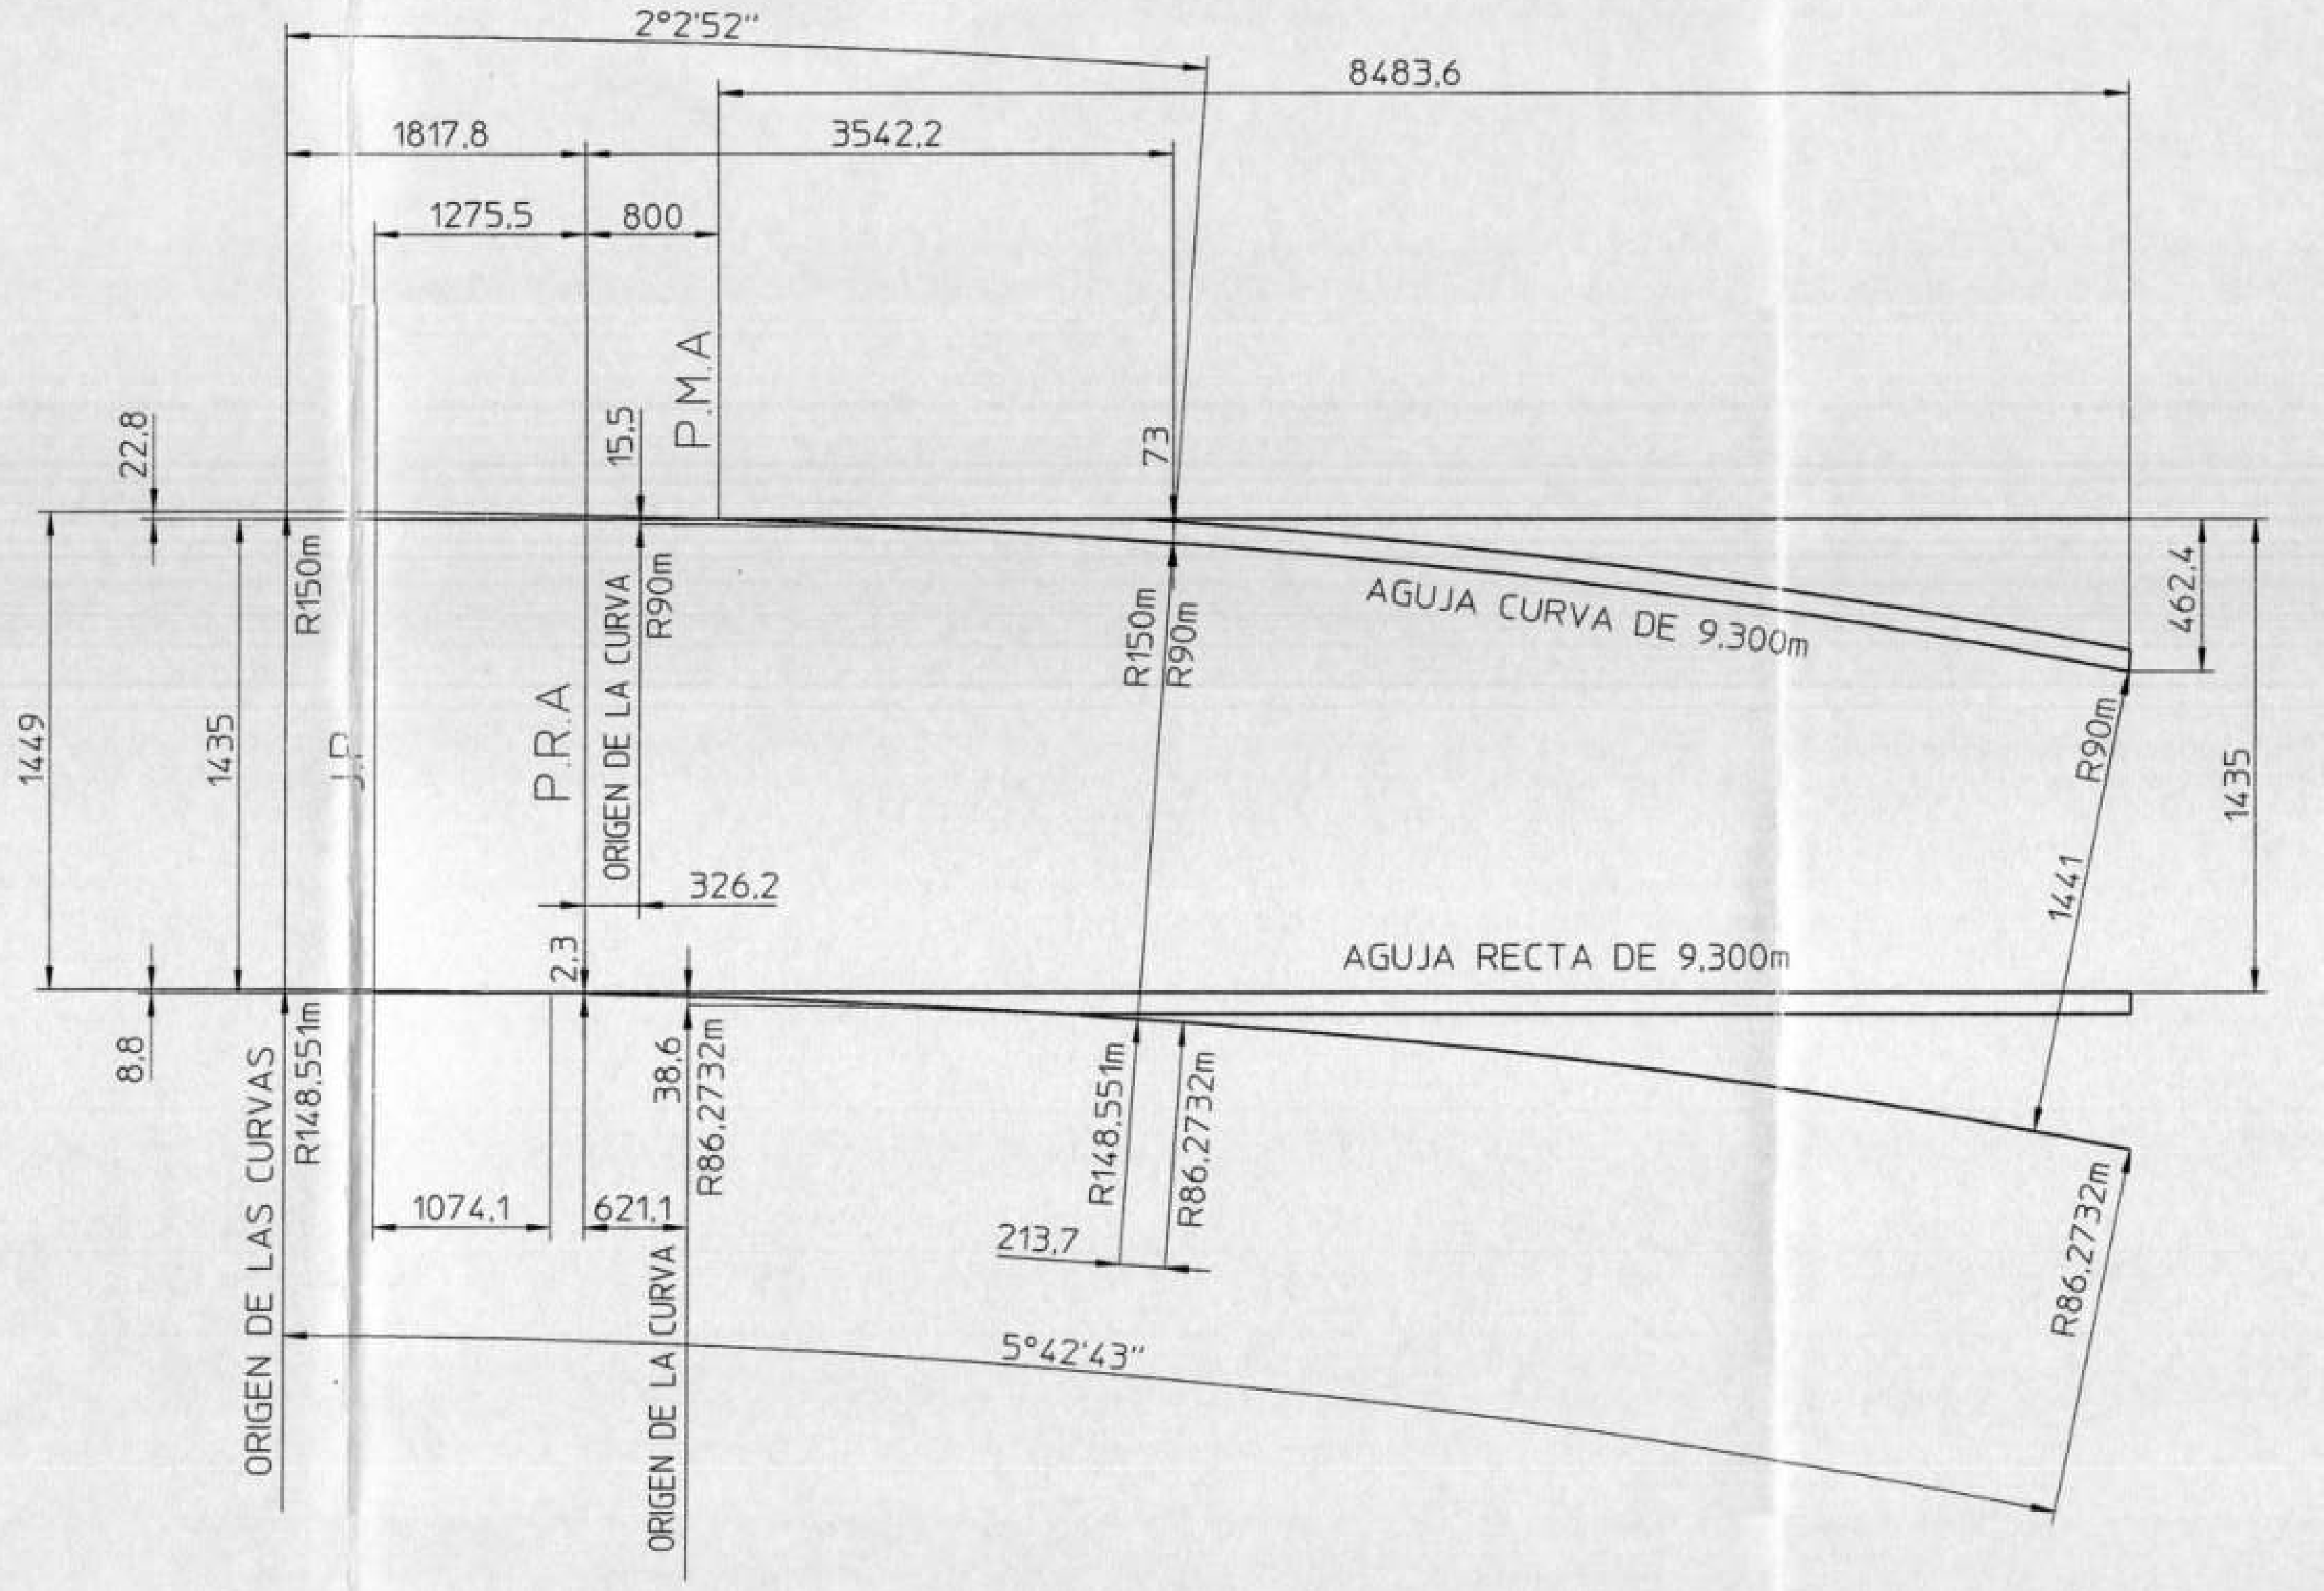

DETALLE DE LAS CABEZAS DE LOS DURMIENTES
AISLADOR SOBRE PLATILLO
Consultar plano N°6.000.000 Mod.0

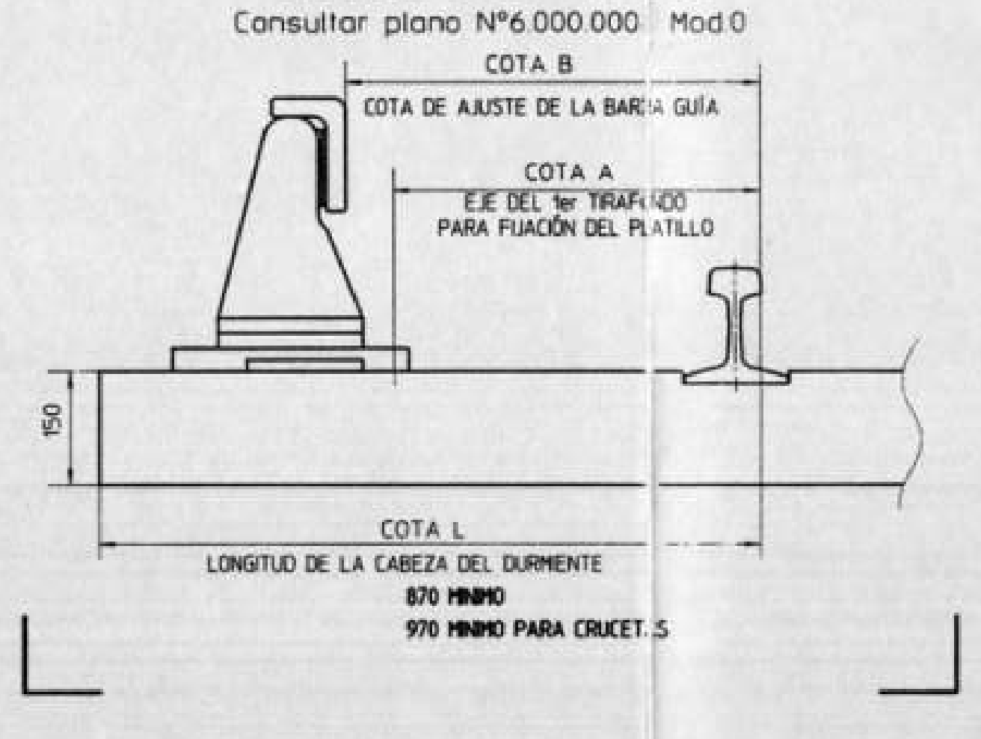
COTA B
COTA DE AJUSTE DE LA BARRA GUÍA
COTA A
EJE DEL 1er TIRAFONDO PARA FIJACIÓN DEL PLATILLO
150
COTA L
LONGITUD DE LA CABEZA DEL DURMIENTE
870 MINIMO
970 MINIMO PARA CRUCETAS

DETALLE DE LAS CABEZAS DE LOS DURMIENTES
AISLADOR SOBRE ZOCLO
Consultar plano N°6.000.0007 Mod.2

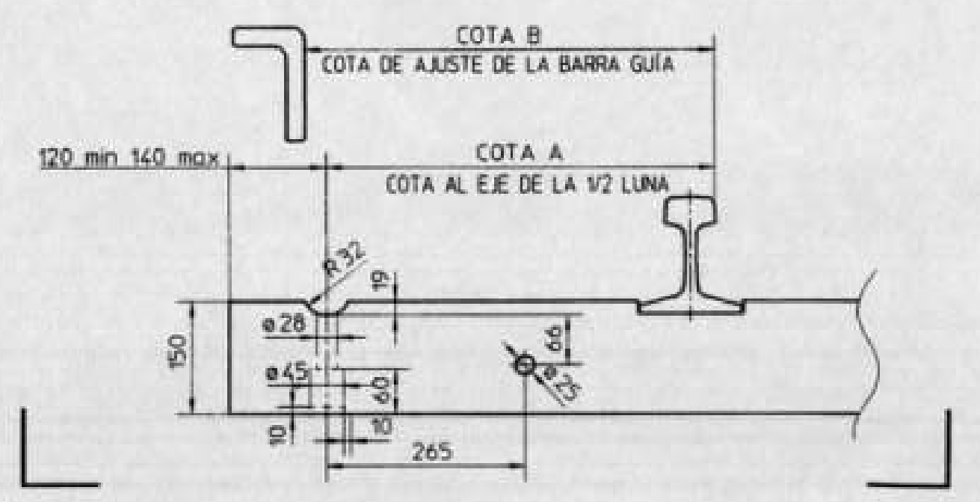

NOTA : Las piezas indicadas con líneas mixtas no forman parte del suministro.

S.T.C.
19/Enero/2007

AUTORIZO : DGCOSTC	APROBO : DGCOSTC	REVISO : DGCOSTC

Nbre Qty	Repère Refer	Symbole Symbol	Désignation des pièces Item	Matière dessin ou norme Material drawing or standard	P. unit. Unit w.

Il faut pour
Requirements for

IMPLANTACIÓN DE VÍA - FIJACIÓN DE VÍA
DESVIO TG.0,13 A LA DERECHA
APARATO 13B - TERMINUS - OBSERVATORIO Linea 1

Date / Date: 19-12-06
Dess. / Drawn: DAAB
Vérif. / Checked:
Homol. / Approved:

Echelle Scale	Type de rail Type of rail	Poids total Total weight	Symbole Symbol
1:50	100RE P 68kg		

Modifications
0 15.12.06 BC0580

vossloh Switch Systems
Vossloh Cogifer

N° plan / Dwg N°: 6 200 6149 0

CE PLAN EST NOTRE PROPRIETE EXCLUSIVE
Il ne peut être reproduit ni copié ni communiqué à des tiers sans notre autorisation écrite (Loi du 11 mars 1932)
THIS DRAWING IS CONFIDENTIAL AND THE COPYRIGHT OF Vossloh Cogifer
And may not be reproduced in any form whatsoever without our written authority (Loi of 11 march 1932)