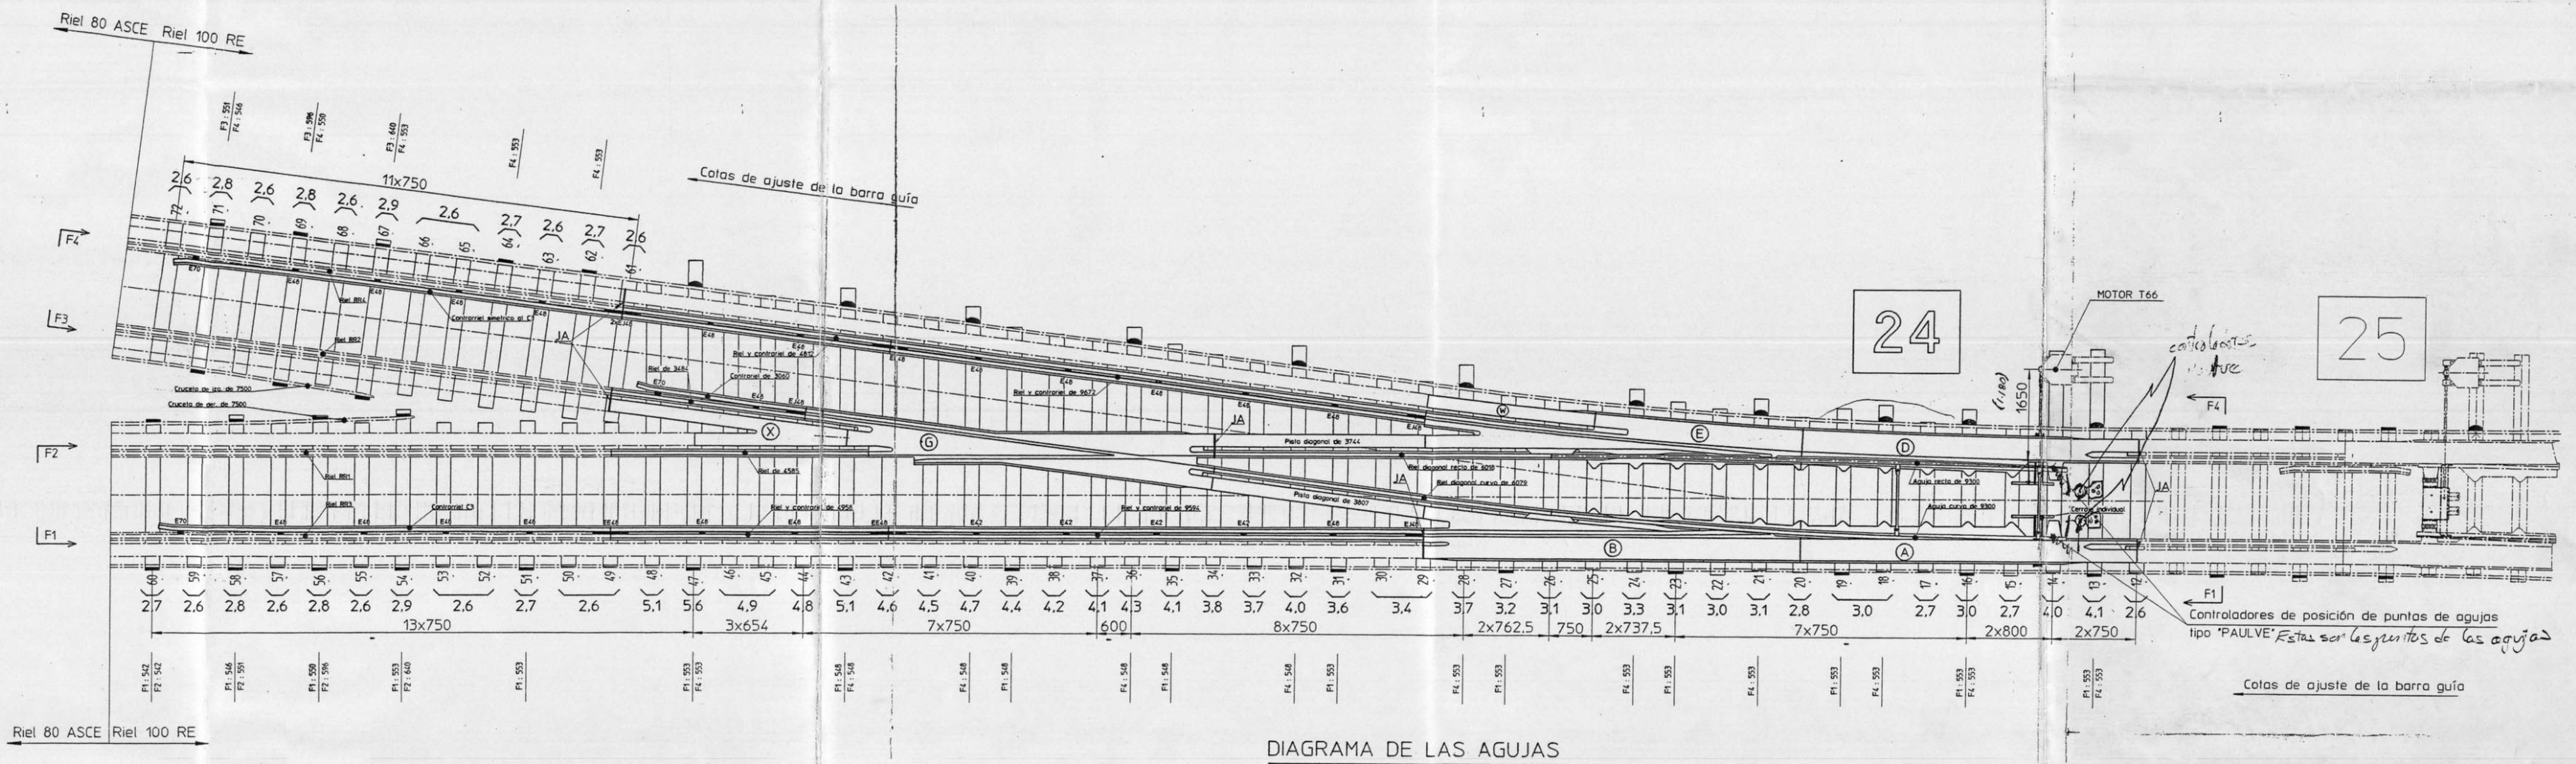


DIAGRAMA DE LAS AGUJAS



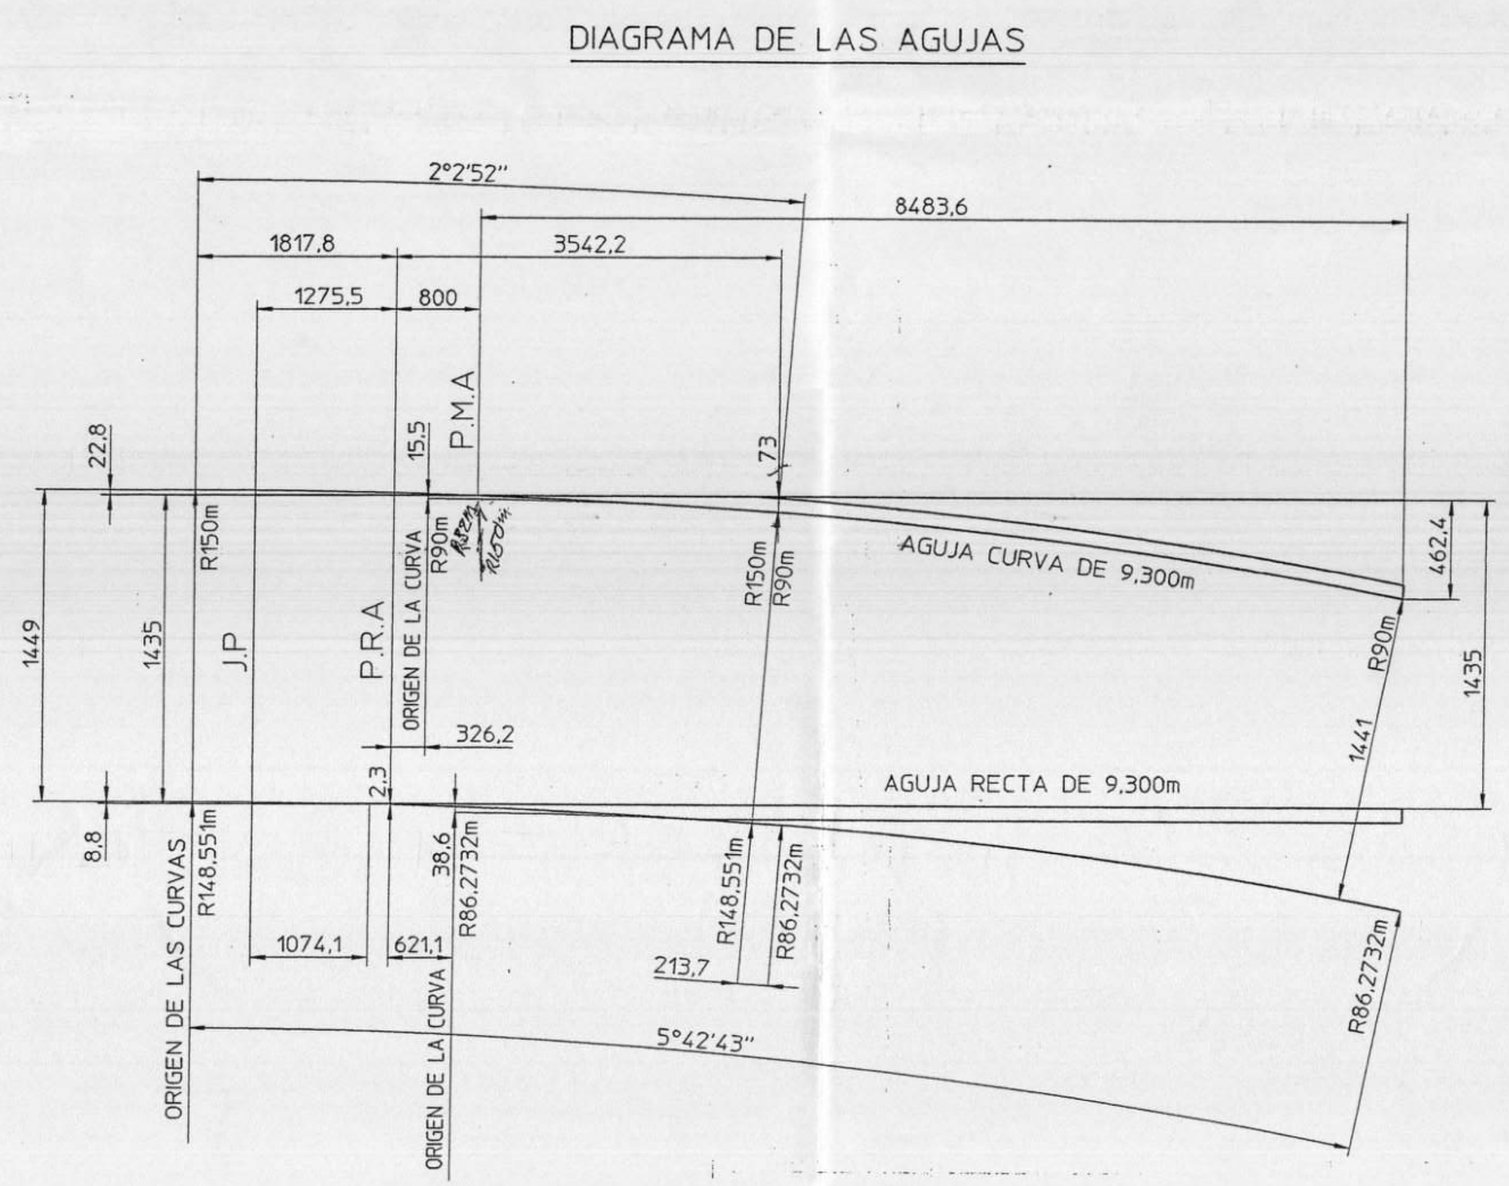


DIAGRAMA DE LAS LÍNEAS DIRECTRICES

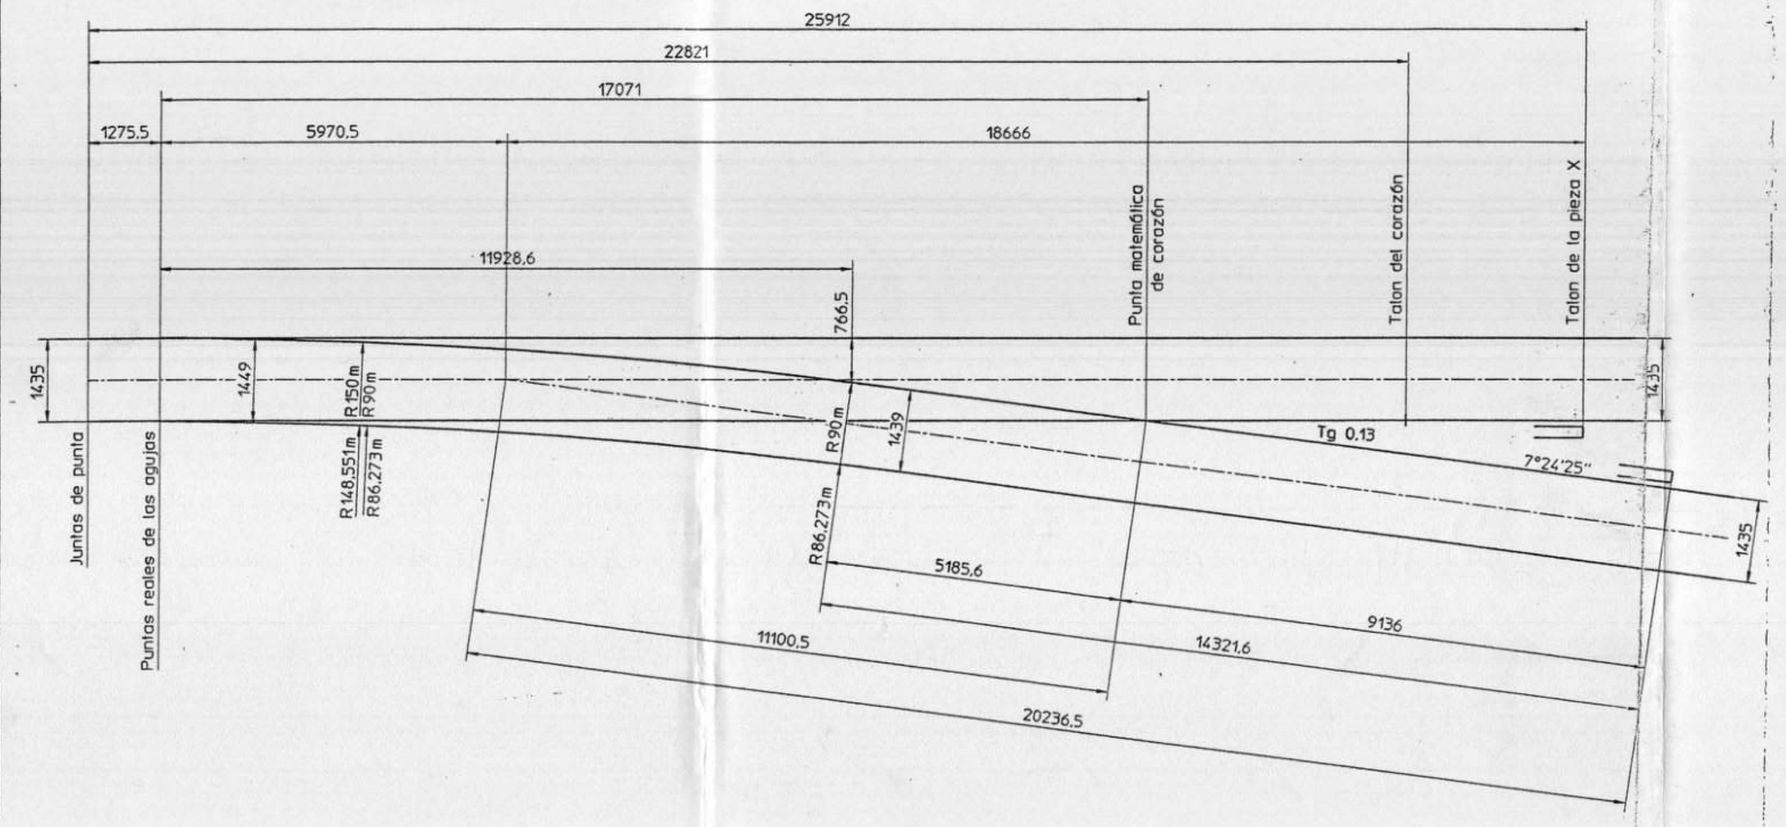


DETALLE DE LAS CABEZAS DE LOS DURMENTES AISLADOR SOBRE PLATILLO

Consultar plano Nº6.000.0008 Mod.0

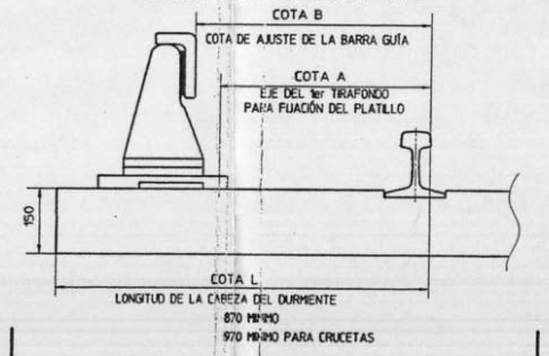

DETALLE DE LAS CABEZAS DE LOS DURMENTES AISLADOR SOBRE ZOCLO

Consultar plano Nº6.000.0007 Mod.2

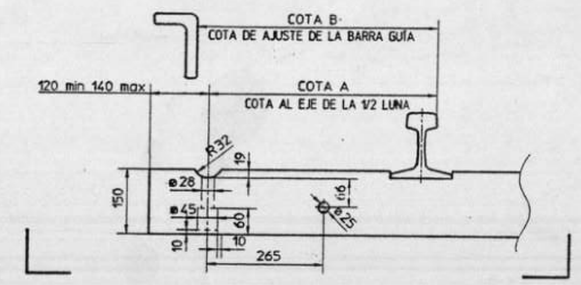

NOTA : Las piezas indicadas con líneas mixtas no forman parte del suministro.

0	19.03.01 BC0371	
Revisó	MODIFICACION	Aprobó COGIFER

COGIFER DEPARTEMENT INDUSTRIE
40, quai de l'Ecluse 78290 Croissy-sur-Seine France

IMPLANTACIÓN DE VÍA - FIJACIÓN DE VÍA
DESVIO TG 0,13 A LA DERECHA
APARATO 24 - BALDERAS SALTO DEL AGUA

SISTEMA DE TRANSPORTE COLECTIVO
Dirección No. 67 C.P. 06070 México D.F.

Escala: 1:50	No. de Plano Cogifer: 16/200/5056	No. de Plano S.T.C.:
Revisó S.T.C.:		Fecha de aprobación S.T.C.
		Dibujó: