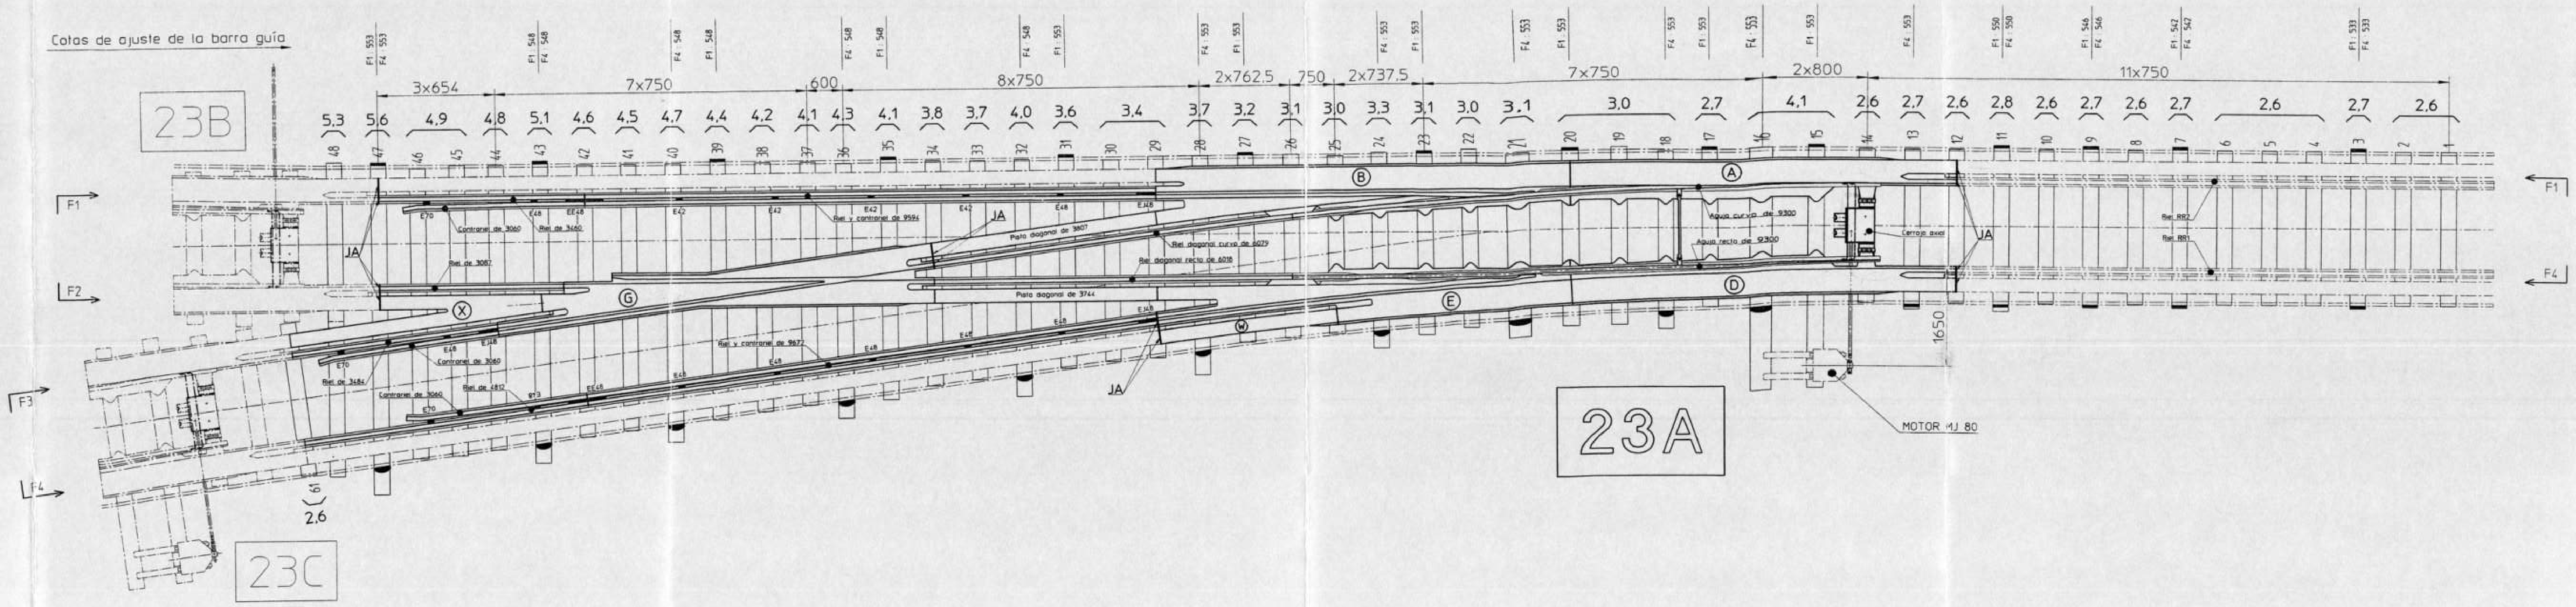

MATERIAL AGREGADO	
Durmiente de 2,60 sin entallado	49,50,52,53,55,57,59,63,65,66,68,70 y 72
Durmiente de 2,70 sin entallado	51,60,62 y 64
Durmiente de 2,80 sin entallado	56,58,69 y 71
Durmiente de 2,90 sin entallado	54 Y 67

DIAGRAMA DE LAS LÍNEAS DIRECTRICES

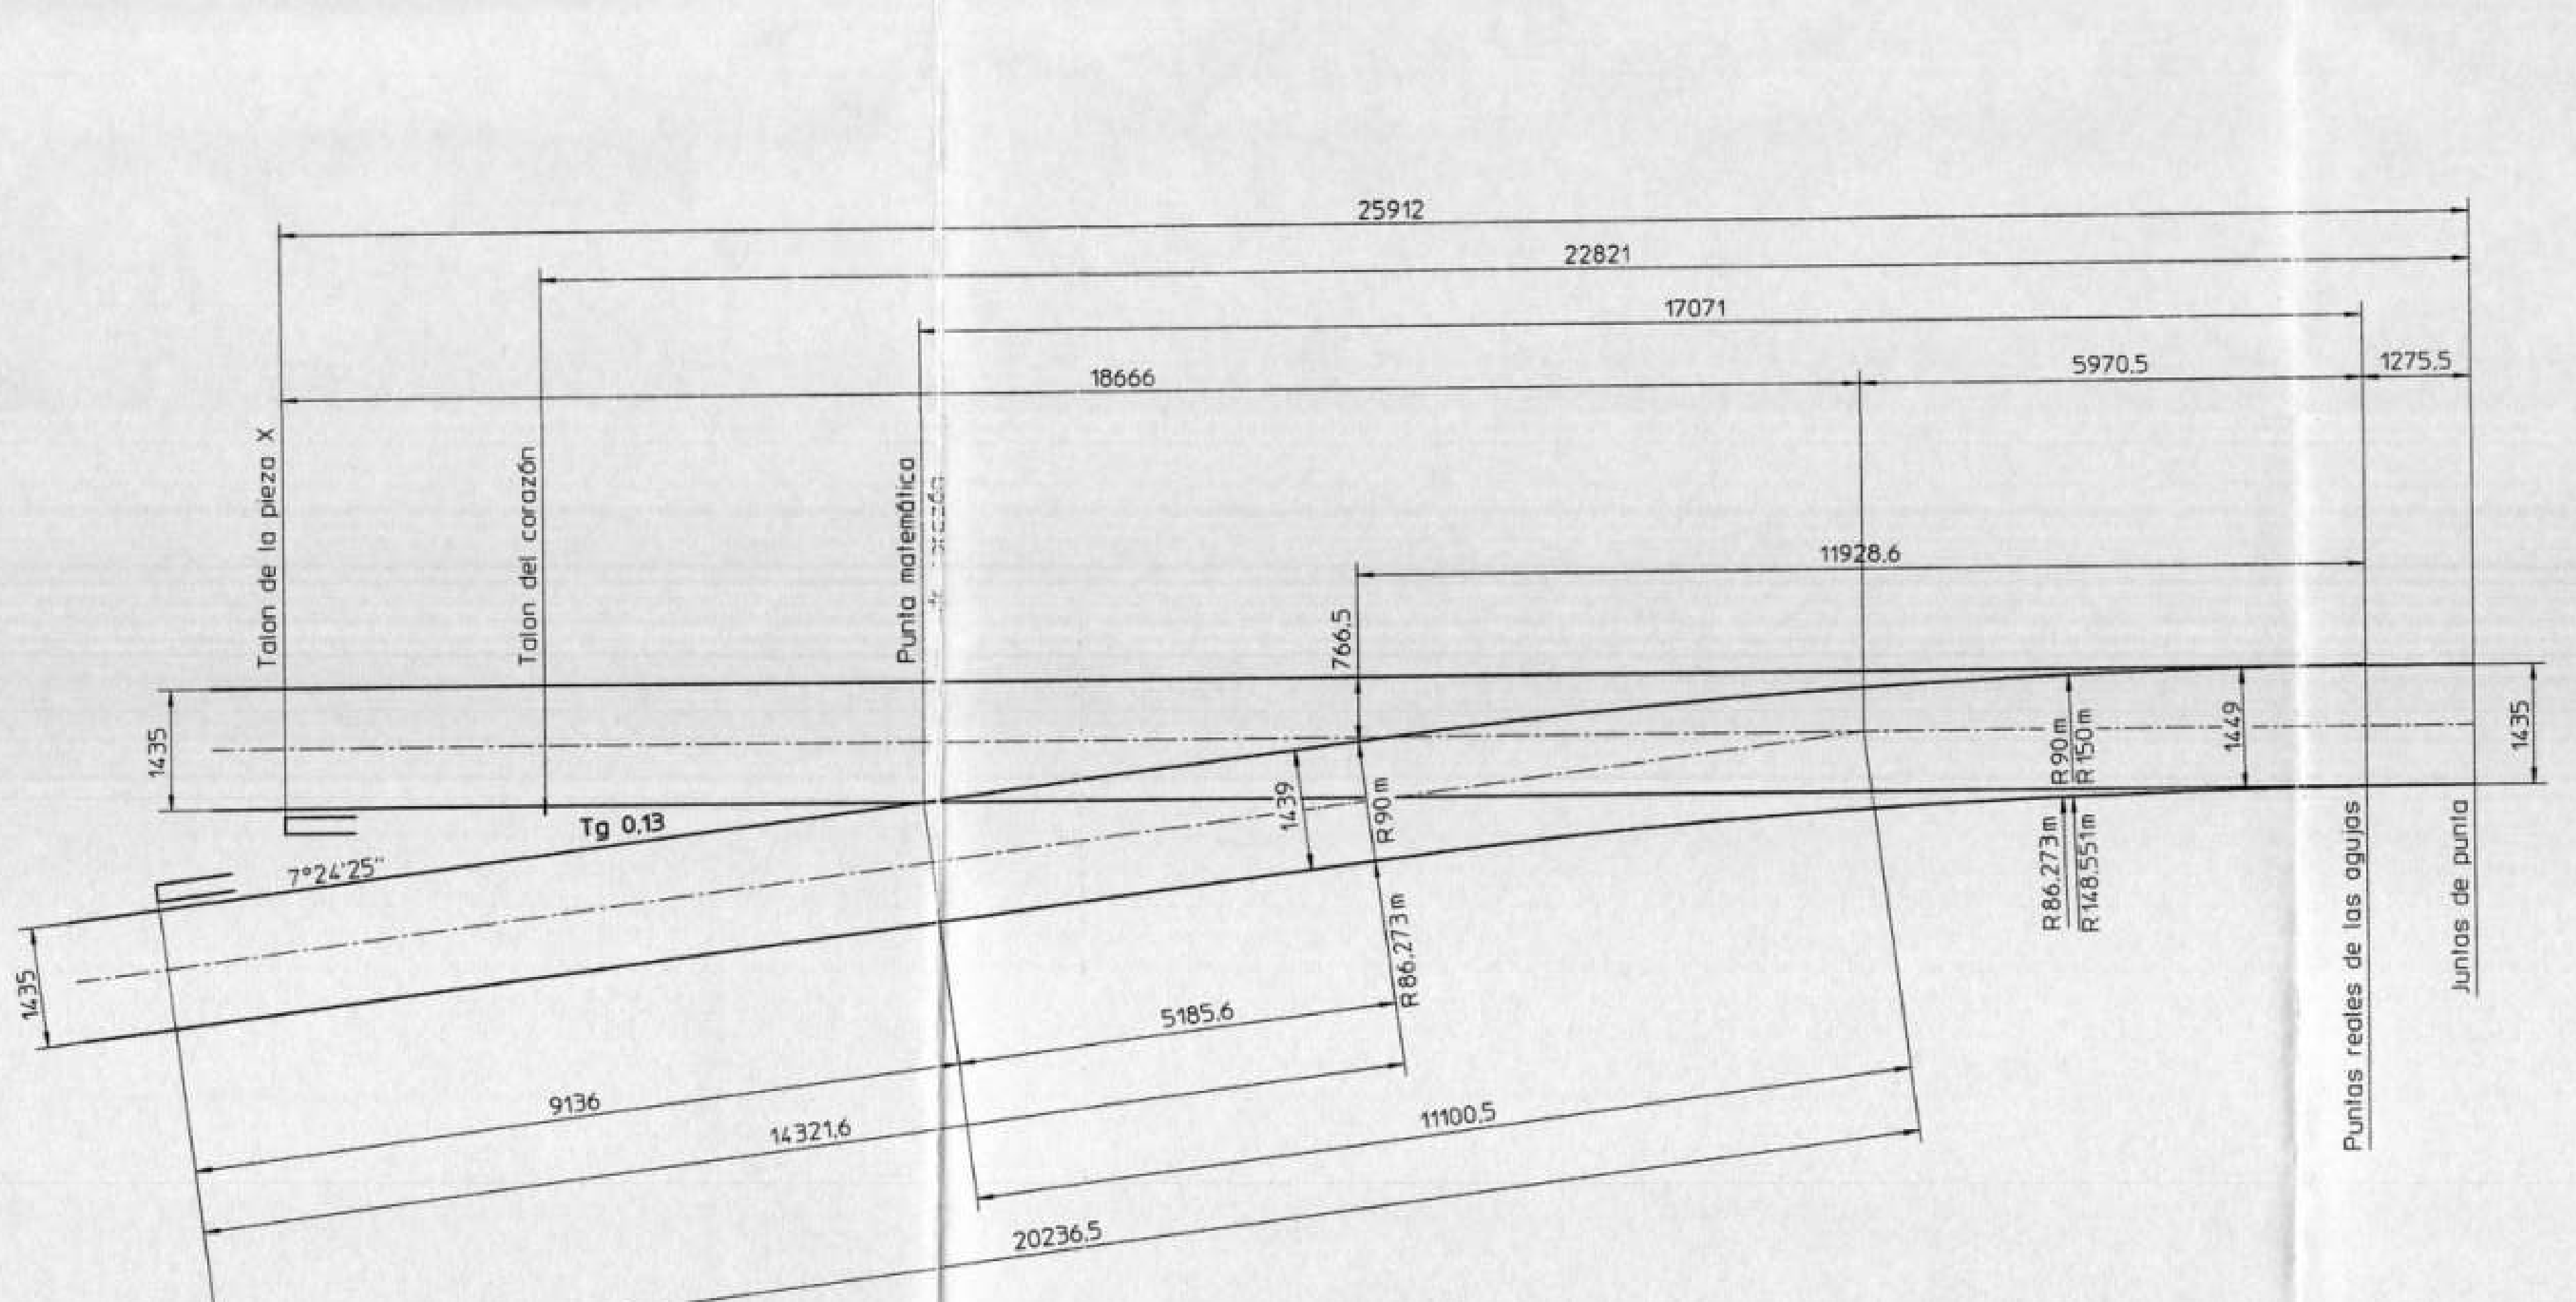

DIAGRAMA DE LAS AGUJAS

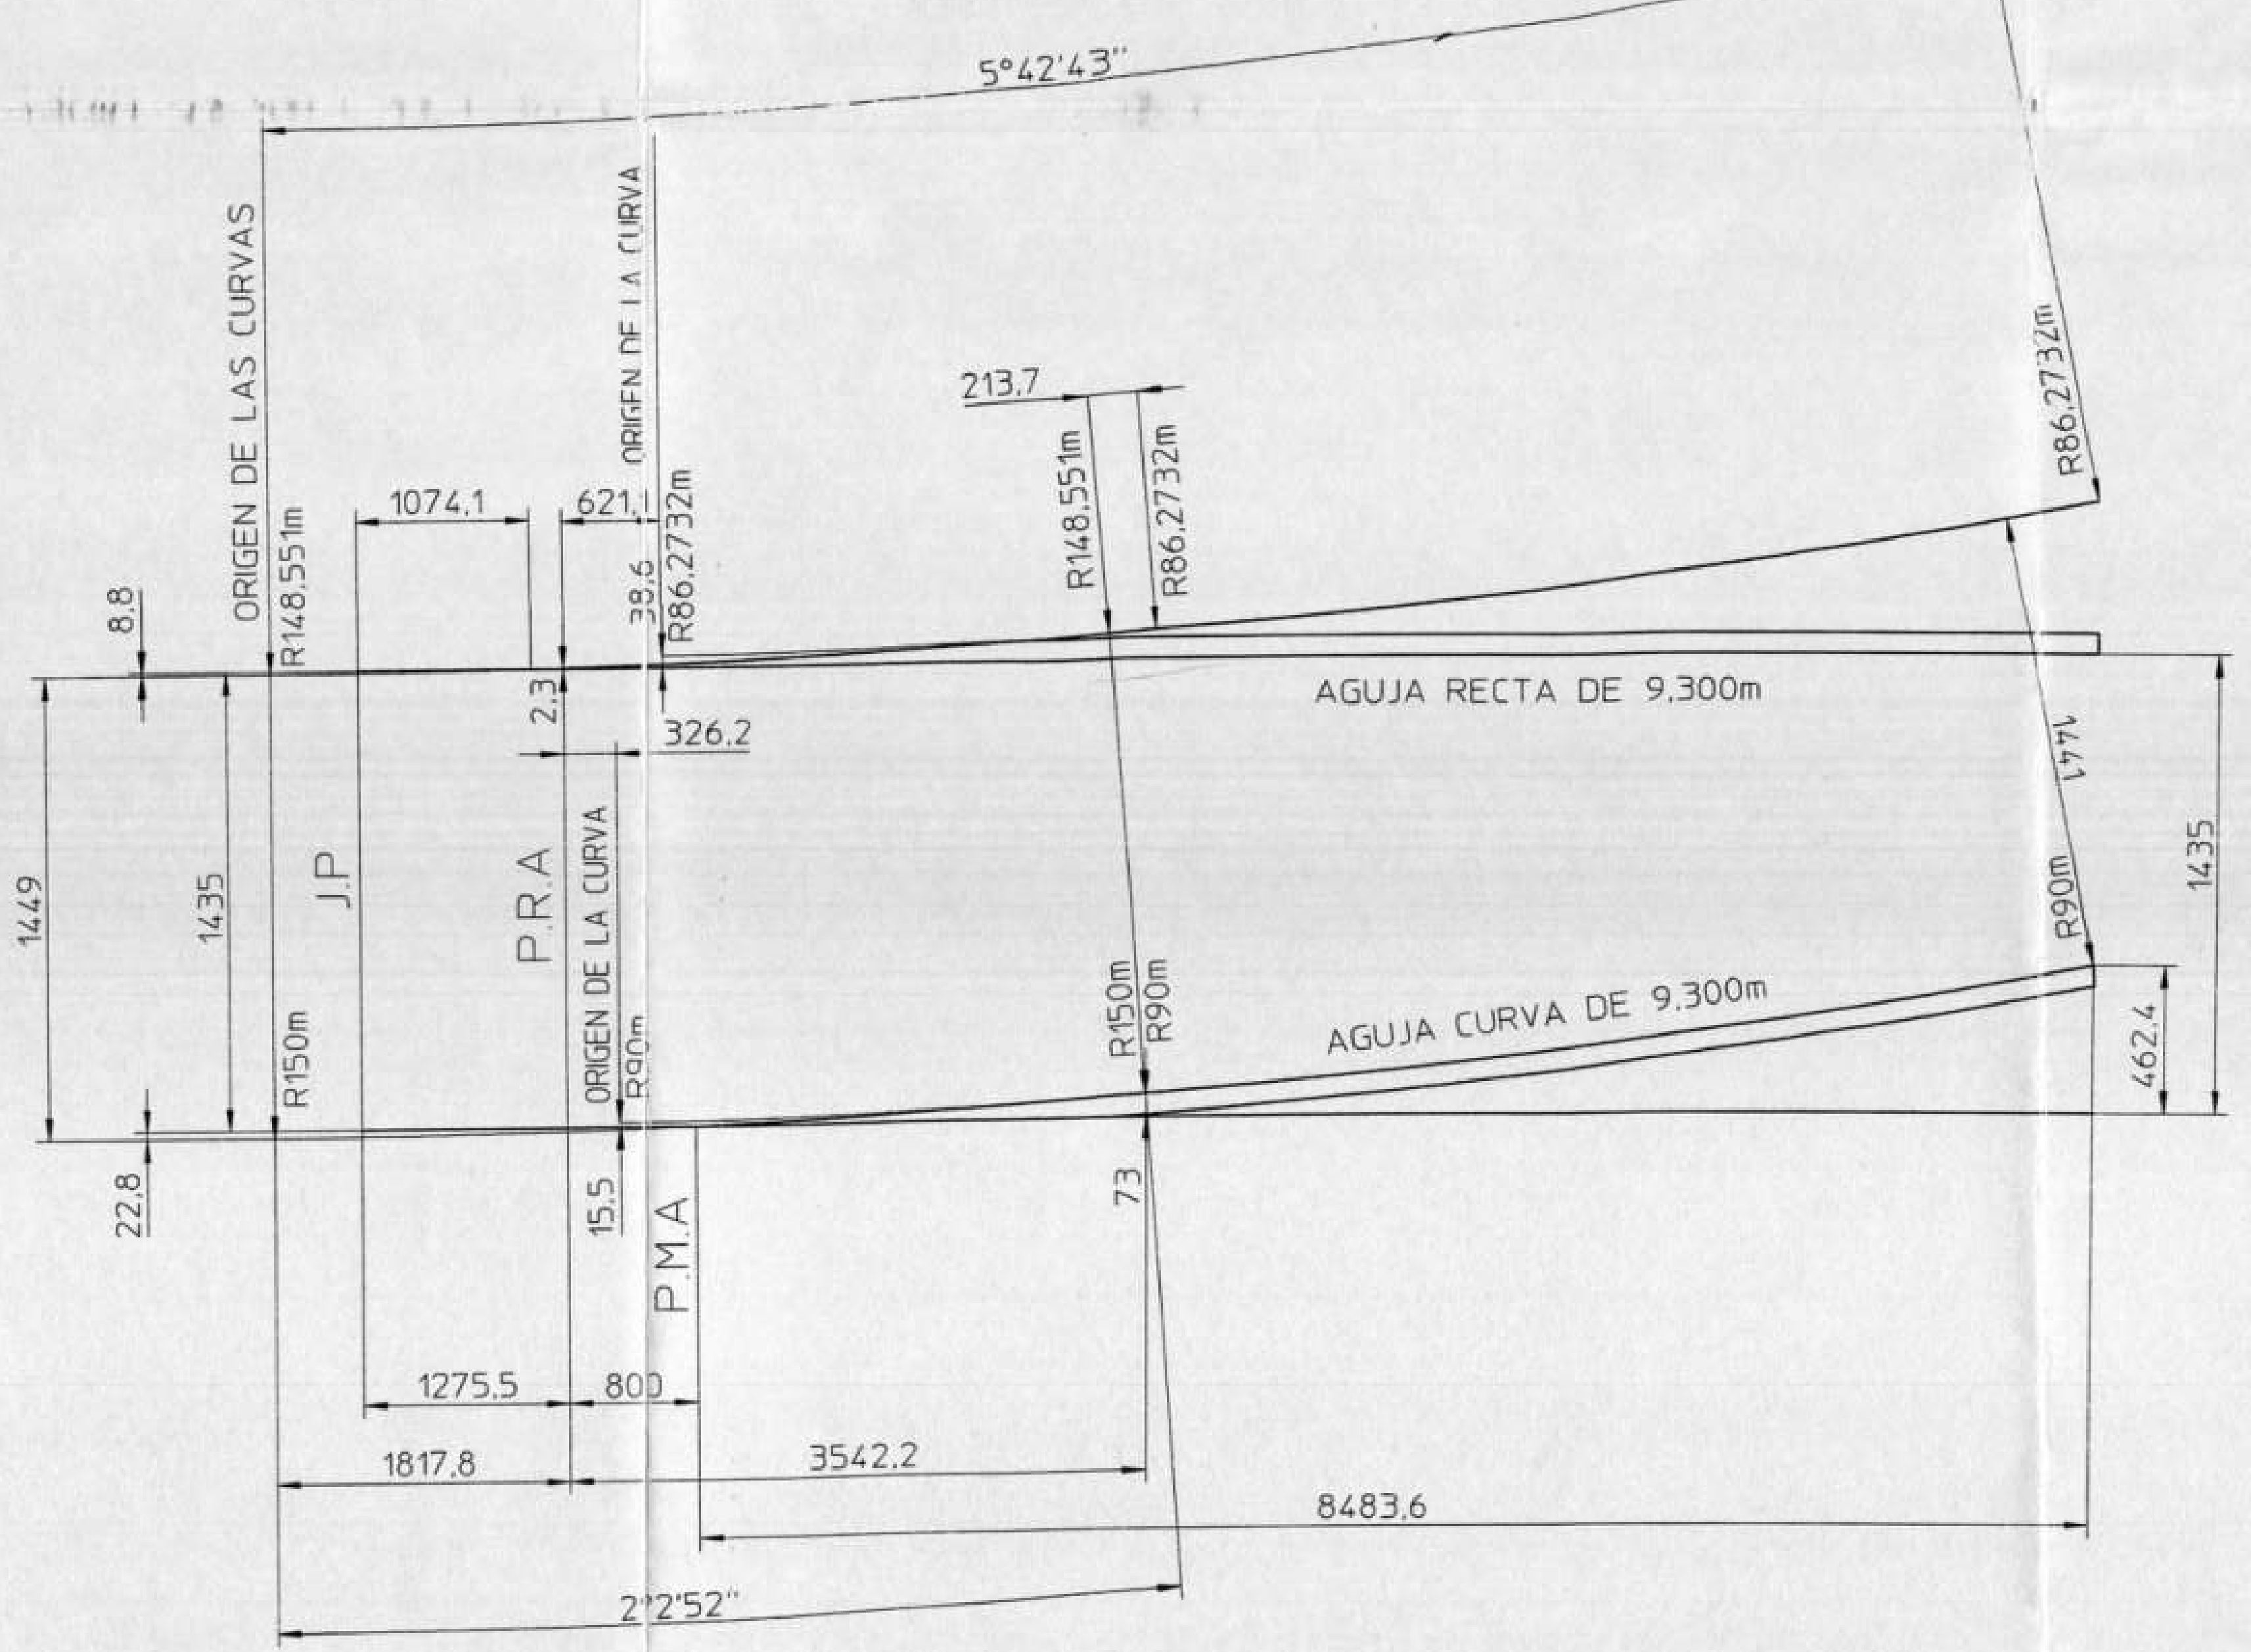

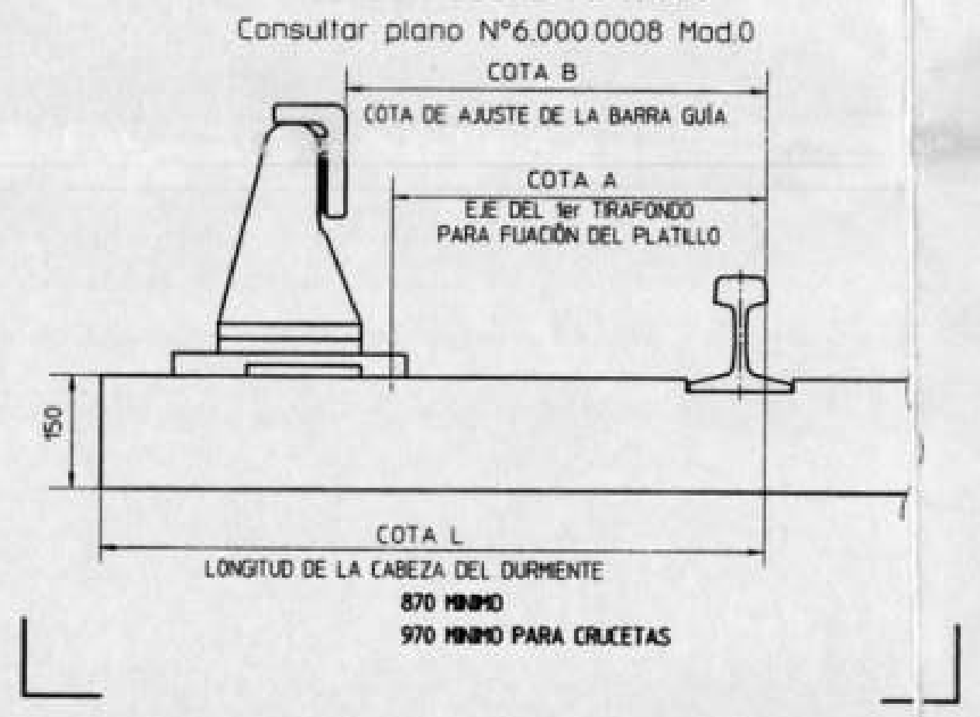
DETALLE DE LAS CABEZAS DE LOS DURMIENTES
AISLADOR SOBRE PLATILLO
Consultar plano N°6.000.0008 Mod.0
COTA B
COTA DE AJUSTE DE LA BARRA GUÍA
COTA A
EJE DEL 1er TIRAFONDO PARA FIJACIÓN DEL PLATILLO
150
COTA L
LONGITUD DE LA CABEZA DEL DURMIENTE
870 MINIMO
970 MINIMO PARA CRUCETAS

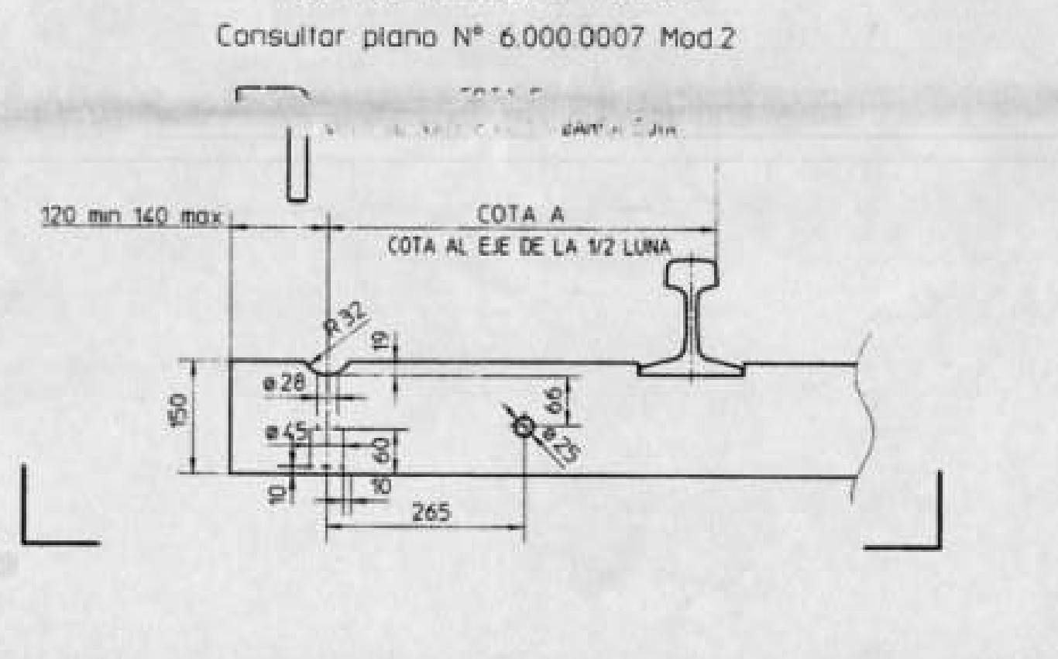
DETALLE DE LAS CABEZAS DE LOS DURMIENTES
AISLADOR SOBRE ZOCLO
Consultar plano N° 6.000.0007 Mod.2

NOTA : Las piezas indicadas con líneas mixtas no forman parte del suministro.

S.T.C.
10/Enero/2007

AUTORIZO : DGCOSTC	APROBO : DGCOSTC	REVISO : DGCOSTC

Nbre Qty	Repère Refer.	Symbole Symbol	Désignation des pièces Item	Matière dessin ou norme Material drawing or standard	P. unit. Unit w.

Il faut pour
Requirements for

IMPLANTACÍON DE VÍA - FIJACIÓN DE VÍA
DESVIO TG.0,13 A LA IZQUIERDA
APARATO 23A - TERMINUS - OBSERVATORIO Linea 1

Date / Date: 20-12-06
Dess. / Drawn: DAAB
Vérif. / Checked:
Homol. / Approved:

Echelle Scale	Type de rail Type of rail	Poids total Total weight	Symbole Symbol
1:50	100RE P 68kg		

Modifications
0 20.12.06 BC0580

Vossloh Switch Systems
Vossloh Cogifer

N° plan / Dwg N°: 6 100 4003 0

CE PLAN EST NOTRE PROPRIETE EXCLUSIVE
Il ne peut être reproduit ni copié ni communiqué à des tiers sans notre autorisation écrite (Loi du 11 mars 1932)
THIS DRAWING IS CONFIDENTIAL AND THE COPYRIGHT OF Vossloh Cogifer
And may not be reproduced in any form whatsoever without our written authority (Law of 11 March 1932)