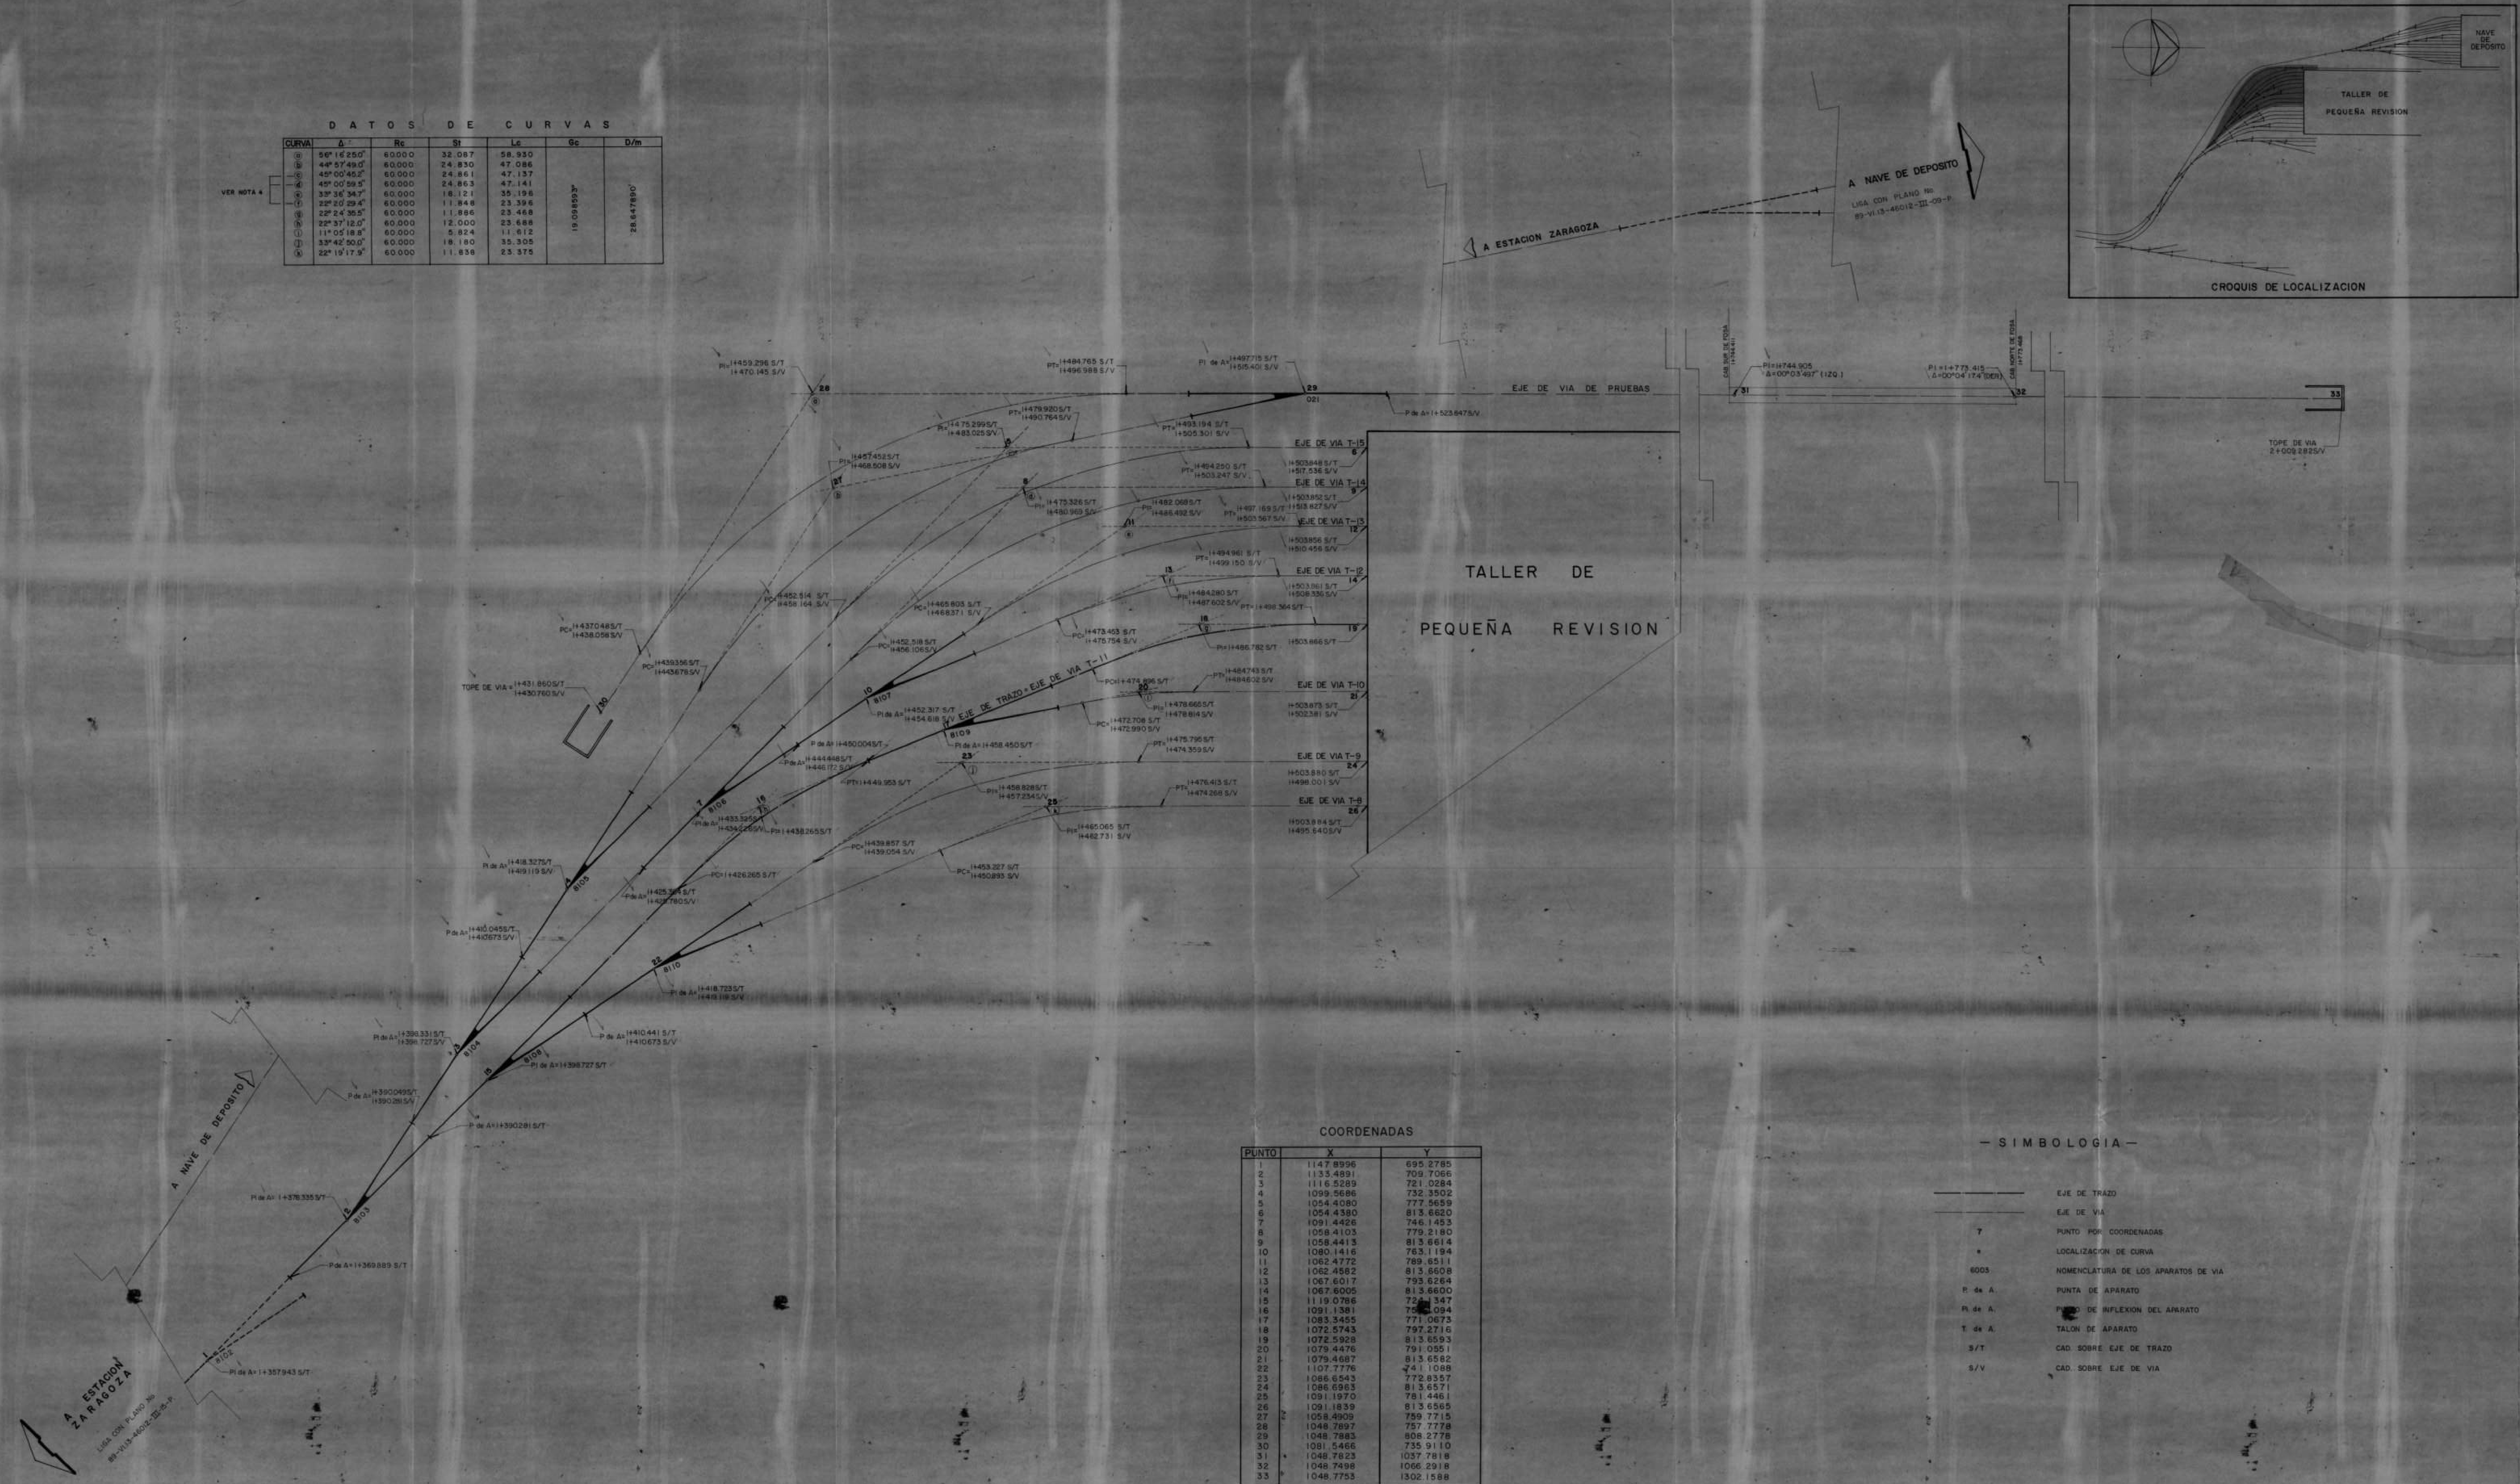
CROQUIS DE LOCALIZACION
NAVE DE DEPOSITO
TALLER DE PEQUEÑA REVISION
A ESTACION ZARAGOZA
A NAVE DE DEPOSITO
LIGA CON PLANO No 89-VI.13-46012-III-09-P
EJE DE VIA DE PRUEBAS
CAB. SUR DE FOSA 1+744.411
PI=1+744.905 Δ=00°03'49.7" (IZQ.)
PI=1+773.415 Δ=00°04'17.4" (DER.)
CAB. NORTE DE FOSA 1+773.468
TOPE DE VIA 2+009.2825/V
PI=1+459.296 S/T 1+470.145 S/V
PT=1+484.765 S/T 1+496.988 S/V
PI de A=1+497.715 S/T 1+515.401 S/V
P de A=1+523.8475/V
PT=1+479.9205/T 1+490.7645/V
PI=1+475.299 S/T 1+483.025 S/V
PT=1+493.194 S/T 1+505.301 S/V
PI=1+457.452 S/T 1+468.508 S/V
PT=1+494.250 S/T 1+503.247 S/V
PI=1+475.326 S/T 1+480.969 S/V
PI=1+482.069 S/T 1+486.492 S/V
PT=1+497.169 S/T 1+503.567 S/V
PT=1+494.961 S/T 1+499.150 S/V
PI=1+484.280 S/T
EJE DE VIA T-15
EJE DE VIA T-14
EJE DE VIA T-13
EJE DE VIA T-12
EJE DE VIA T-10
EJE DE VIA T-9
EJE DE VIA T-8
1+503.848 S/T 1+517.536 S/V
1+503.852 S/T 1+513.827 S/V
1+503.856 S/T 1+510.456 S/V
1+503.861 S/T 1+508.336 S/V
EJE DE TRAZO = EJE DE VIA T-11
TOPE DE VIA=1+431.860S/T 1+430.760S/V
TALLER DE PEQUEÑA REVISION
A ESTACION ZARAGOZA
LIGA CON PLANO No 89-VI.13-46012-III-09-P
A NAVE DE DEPOSITO
021
8101
8103
8104
8105
8106
8107
8108
8109
8110

N O T A S :

1- EL ORIGEN DE CADENAMIENTOS 1+176.952 ESTA UBICADO EN LA P. del A. 8201 LOCALIZADO AL SUR DEL TALLER DE PEQUEÑA REVISION.

2- EL ORIGEN DE COORDENADAS CORRESPONDE AL PUNTO 1 DE LA TANGENTE AUXILIAR G-11 LOCALIZADO A 10.265 MTS. DE LA CABECERA DE LA NAVE DE DEPOSITO.

3- TODOS LOS CADENAMIENTOS ESTAN REFERIDOS AL EJE DE TRAZO DEL TALLER DE PEQUEÑA REVISION , EXCEPTO LOS INDICADOS.

4.-LAS CURVAS c , d , f NO FUERON IMPLANTADAS DE ACUERDO A PROYECTO POR LO QUE SUS DATOS REALES DE CAMPO SON LOS SIGUIENTES.

ⓒ	ⓓ	ⓕ
Δ = 45° 01' 30"	Δ = 44° 59' 00"	Δ = 22° 17' 28"
Rc = 60. 000 m.	Rc = 60. 000 m.	Rc = 60. 000 m.
St = 24. 868 m.	St = 24. 843 m.	St = 11. 821 m.
Lc = 47. 150 m.	Lc = 47. 106 m.	Lc = 23. 343 m.
Gc = 19. 098593°	Gc = 19. 098593°	Gc = 19. 098593°
D/M 28. 647890'	D/M 28. 647890'	D/M 28. 647890'

D A T O S D E C U R V A S

CURVA	Δ	Rc	St	Lc	Gc	D/m
ⓐ	56° 16' 25.0"	60.000	32.087	58.930	19.098593°	28.647890'
ⓑ	44° 57' 49.0"	60.000	24.830	47.086		
ⓒ	45° 00' 45.2"	60.000	24.861	47.137		
ⓓ	45° 00' 59.5"	60.000	24.863	47.141		
ⓔ	33° 36' 34.7"	60.000	18.121	35.196		
ⓕ	22° 20' 29.4"	60.000	11.848	23.396		
ⓖ	22° 24' 35.5"	60.000	11.866	23.468		
ⓗ	22° 37' 12.0"	60.000	12.000	23.688		
ⓘ	11° 05' 18.8"	60.000	5.824	11.612		
ⓙ	33° 42' 50.0"	60.000	18.180	35.305		
ⓚ	22° 19' 17.9"	60.000	11.838	23.375		

VER NOTA 4

COORDENADAS

PUNTO	X	Y
1	1147.8996	695.2785
2	1133.4891	709.7066
3	1116.5289	721.0284
4	1099.5686	732.3502
5	1054.4080	777.5659
6	1054.4380	813.6620
7	1091.4426	746.1453
8	1058.4103	779.2180
9	1058.4413	813.6614
10	1080.1416	763.1194
11	1062.4772	789.6511
12	1062.4582	813.6608
13	1067.6017	793.6264
14	1067.6005	813.6600
15	1119.0786	72[illegible]1347
16	1091.1381	75[illegible]094
17	1083.3455	771.0673
18	1072.5743	797.2716
19	1072.5928	813.6593
20	1079.4476	791.0551
21	1079.4687	813.6582
22	1107.7776	741.1088
23	1086.6543	772.8357
24	1086.6963	813.6571
25	1091.1970	781.4461
26	1091.1839	813.6565
27	1058.4909	759.7715
28	1048.7897	757.7778
29	1048.7883	808.2778
30	1081.5466	735.9110
31	1048.7823	1037.7818
32	1048.7498	1066.2918
33	1048.7753	1302.1588

— S I M B O L O G I A —

———	EJE DE TRAZO
———	EJE DE VIA
7	PUNTO POR COORDENADAS
a	LOCALIZACION DE CURVA
6003	NOMENCLATURA DE LOS APARATOS DE VIA
P. de A.	PUNTA DE APARATO
Pi. de A.	PUNTO DE INFLEXION DEL APARATO
T. de A.	TALON DE APARATO
S/T	CAD. SOBRE EJE DE TRAZO
S/V	CAD. SOBRE EJE DE VIA

No.	M O D I F I C A C I O N	F E C H A	A P R O B O
1-	SE COMPLEMENTA CON PI'S 1+744.905 Y 1+773.415, CON LOS CADENAMIENTOS 1+744.411 Y 1+773.468 DE LA FOSA DE REVISION Y CON LAS COORDENADAS 31, 32 Y 33, DEBIDO A LA IMPLANTACION DE EJES DE VIA EN CAMPO	14/DICIEMBRE/89	ING. ISMAEL GONZALEZ T.

DEPARTAMENTO DEL DISTRITO FEDERAL
STC
SISTEMA DE TRANSPORTE COLECTIVO

ING. GERARDO FERRANDO BRAVO
DIRECTOR GENERAL

ING. FILIBERTO ZEPEDA TIJERINA
DIRECTOR DE OPERACION

ELECTRO METRO S.A.
PROYECTO

PROYECTO:
REALINEACION Y RENIVELACION DE VIAS EN OPERACION
METRO

ING. PABLO GUERRA CARDENAS

ING. ALBERTO GONZALEZ CENICEROS

TALLERES ZARAGOZA
IMPLANTACION DE VIA-TRAZO
TRAMO COLA ZARAGOZA—T PEQUEÑA REVISION
VIAS DE ACCESO A TALLER DE PEQUEÑA REVISION
(VIAS T8 A T15 Y VIA DE PRUEBAS)

ARQ. JOSE LUIS BUENDIA M.

ING. LUIS BERNARDO RODRIGUEZ E.

ING. SERGIO RUVALCABA MONCAYO

STC. ARQ. MANUEL MEZA ZATARAIN	ESCALA 1:200	ING. ISMAEL GONZALEZ T.
STC. ING. SALOMON SOLAY ZYMAN	ACOTACIONES EN METROS	ING. J. BARRIOS R. / ING. B. CASTILLO S.
STC. ING. ROBERTO CASTAÑEDA CHAVEZ	FECHA OCTUBRE/ 89	PLANO No MOD. 1 89-VI.13-46012-III-10-P.
STC. ING. ERASMO CUATECONTZI CASTELLANOS		
STC. ING. MARCO A. ROCHA ORBINA	STC. ING. ALFREDO NAVARRETE YAÑEZ	INPLAT. ING. FERNANDO CASTRO C.

(0.90 X 2.11 mts.)